


SHAMA & VERONIE

Architecture & Interior Design
PORTFOLIO

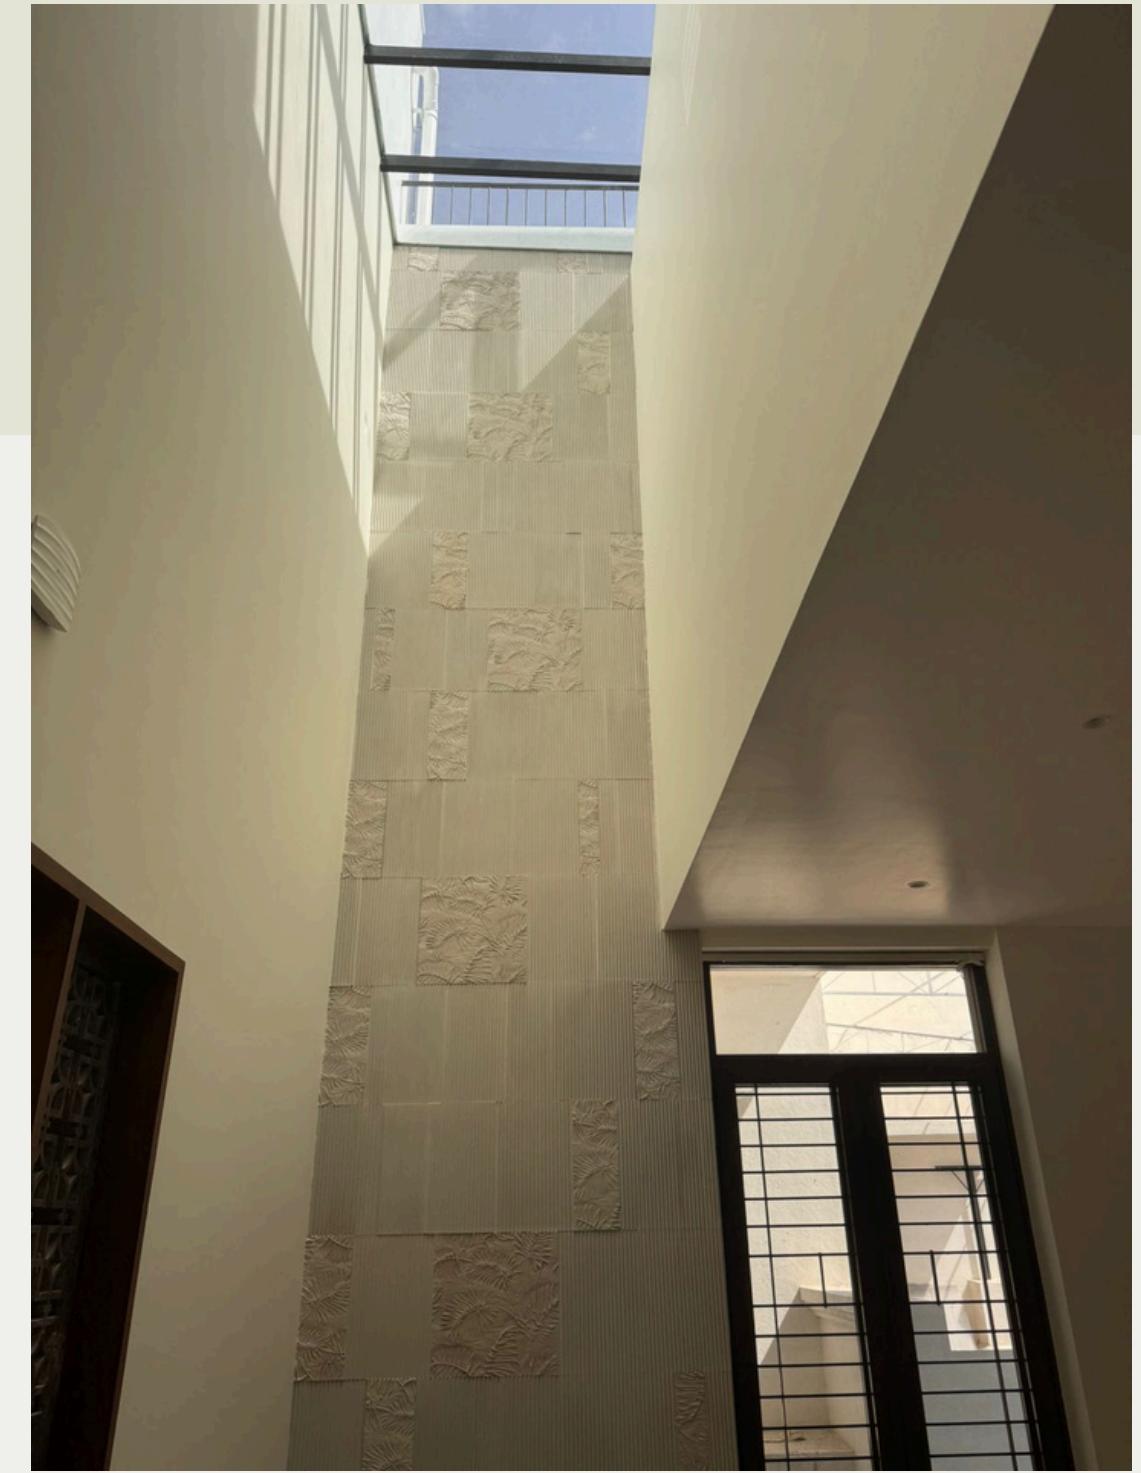

We are an architectural duo with combined expertise in architecture, interior design, urban design, and art. We have handled projects as lead architects across the cities of Bangalore, Chennai, Hyderabad and Mangalore.

INTERIOR DESIGN

1. Flowing Tree Apartments
2. Shoba Royal Pavilion
3. Rajithadri
4. Srinivasa Textiles Work Pods

ARCHITECTURE

1. Keshav Murthy Residence - Indiranagar
2. SDM Eye Hospital Mangalore - Facade Design
3. Veerabhavana, Mangalore

RENOVATION

1. Egmore Kitchen Renovation
2. KSE Farmhouse

ART



1. The Entrance Cafe, Kilpauk
2. Mezze Madras, Anna Nagar



INTERIORS



LIVING ROOM

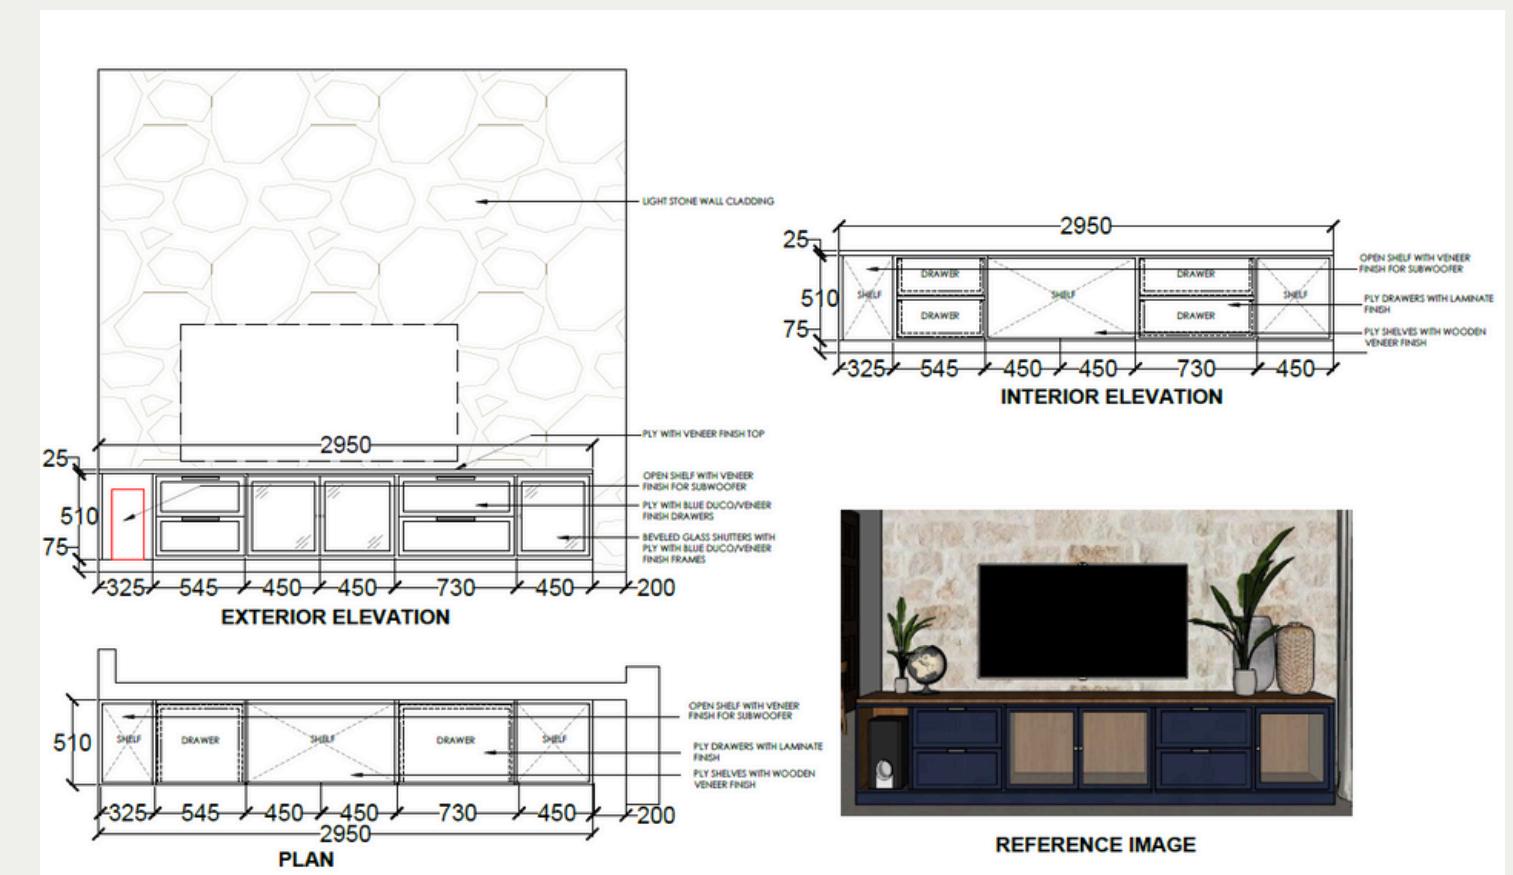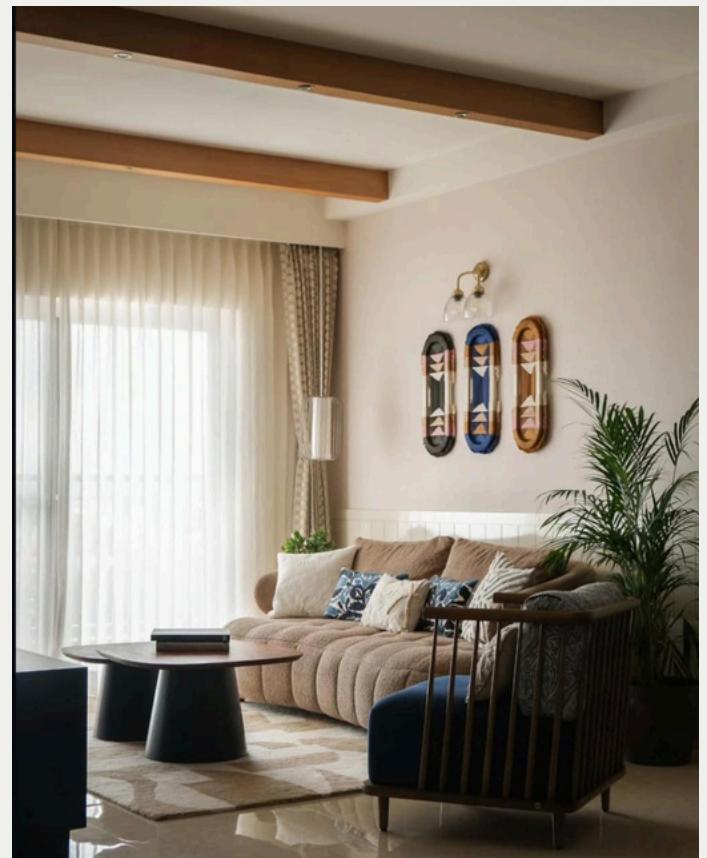


REFERENCE IMAGE

1 FLOWING TREE APARTMENTS, BANGALORE

SHAMA & VERONIE









KITCHEN

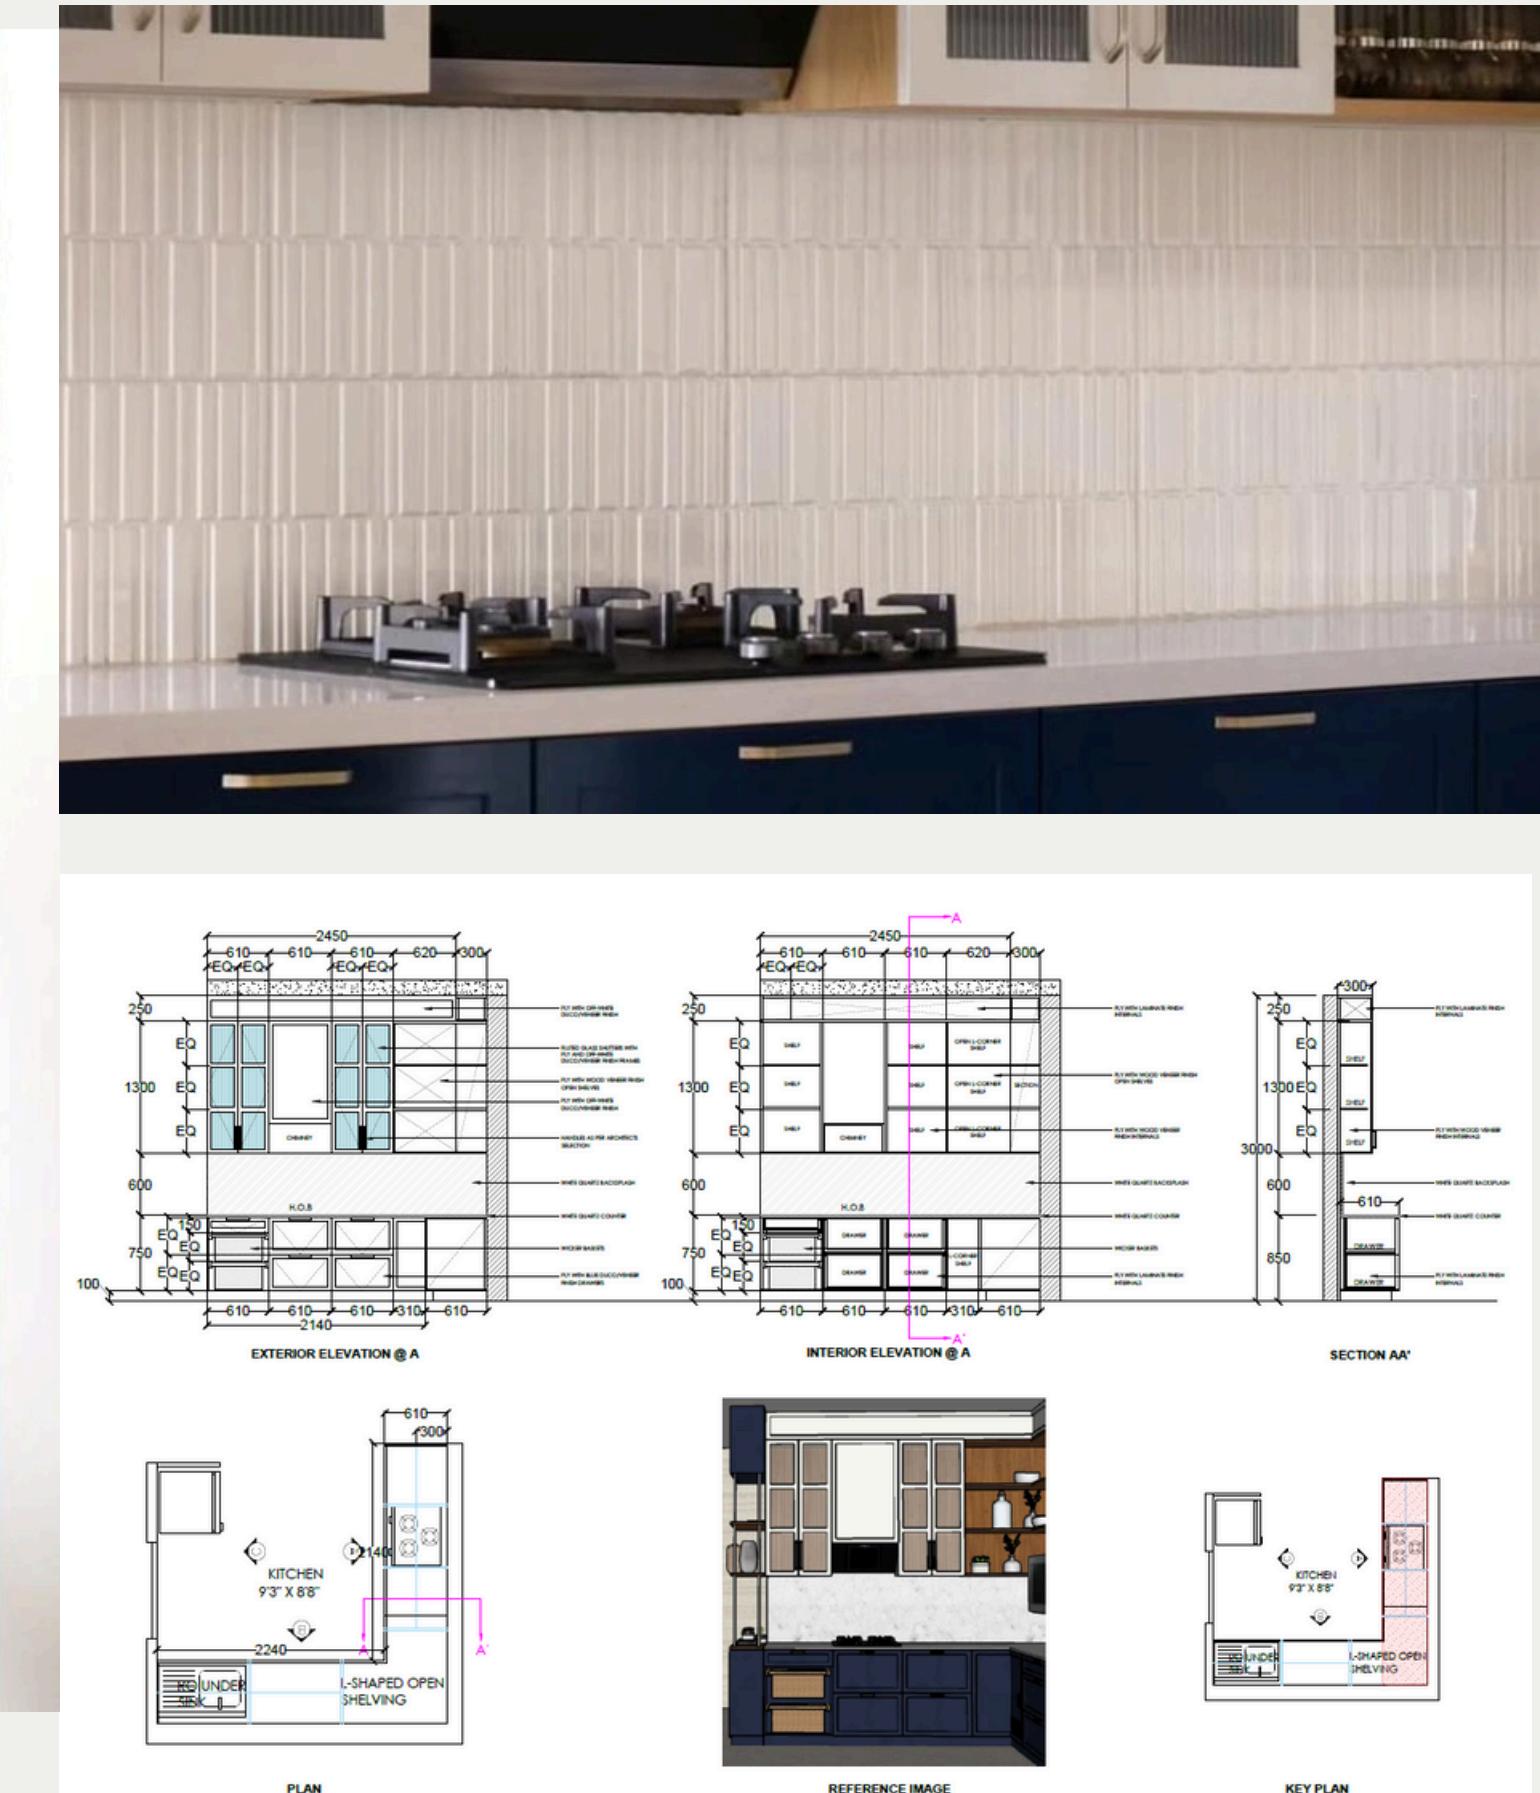

*PROJECT LEAD IN STUDIO SKAPA ARCHITECTS






MASTER BEDROOM

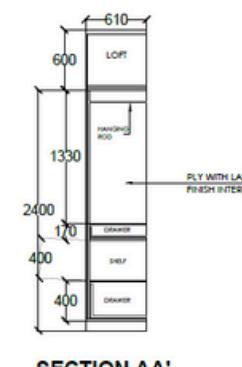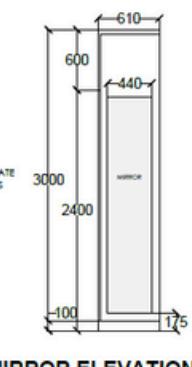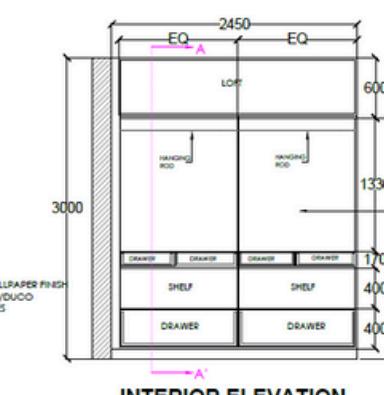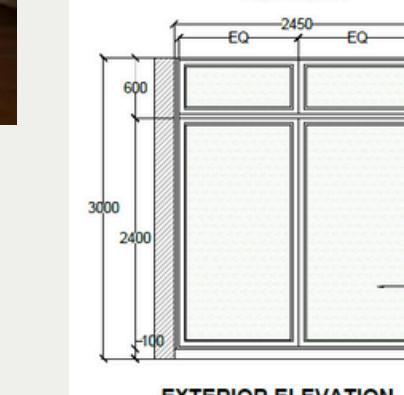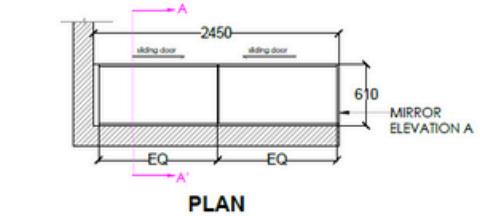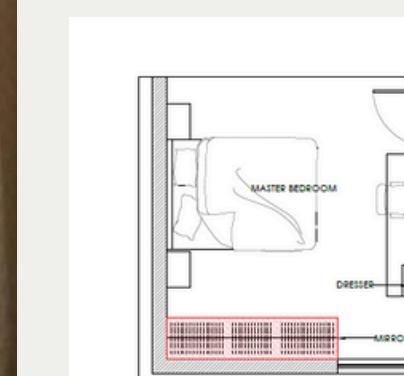

1 FLOWING TREE APARTMENTS, BANGALORE

SHAMA & VERONIE

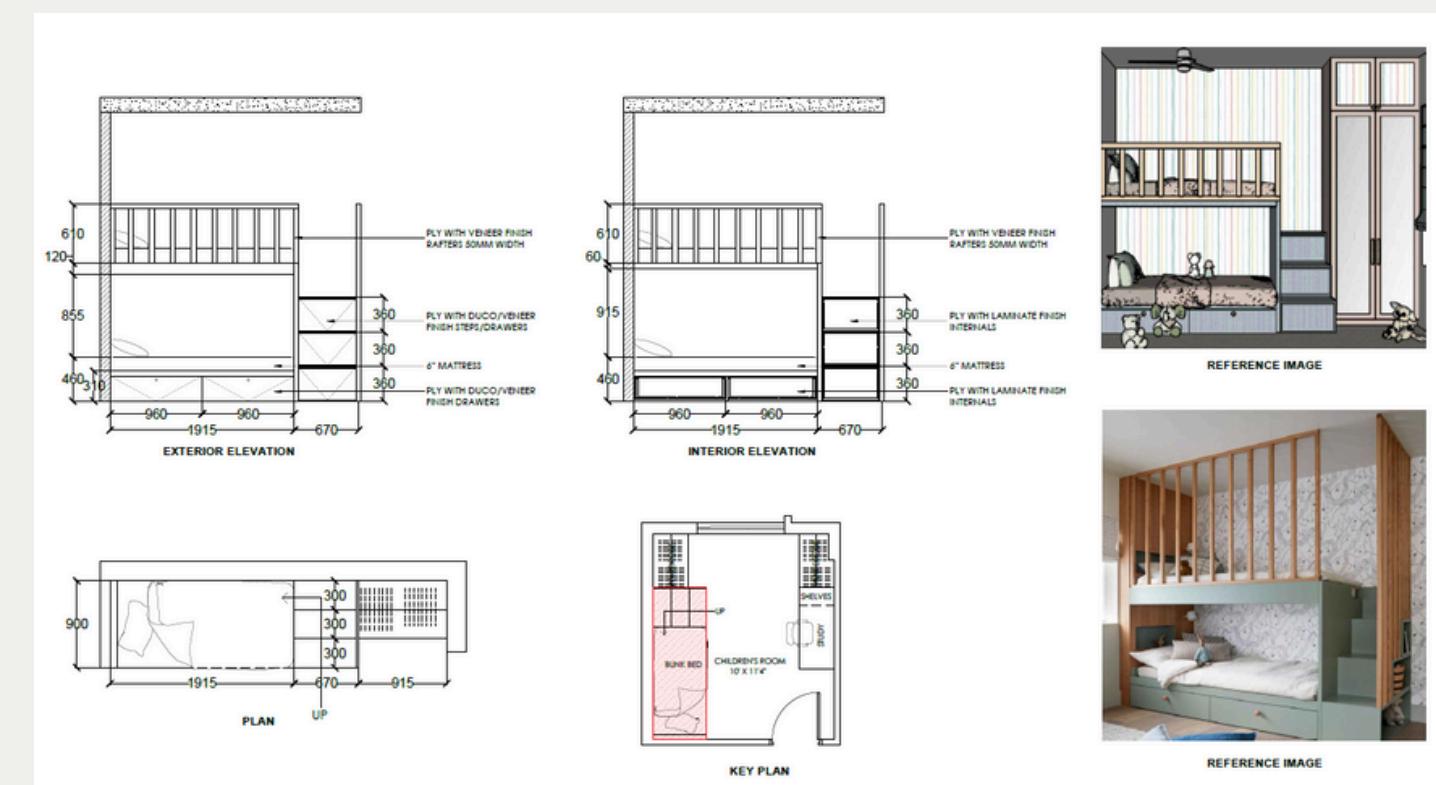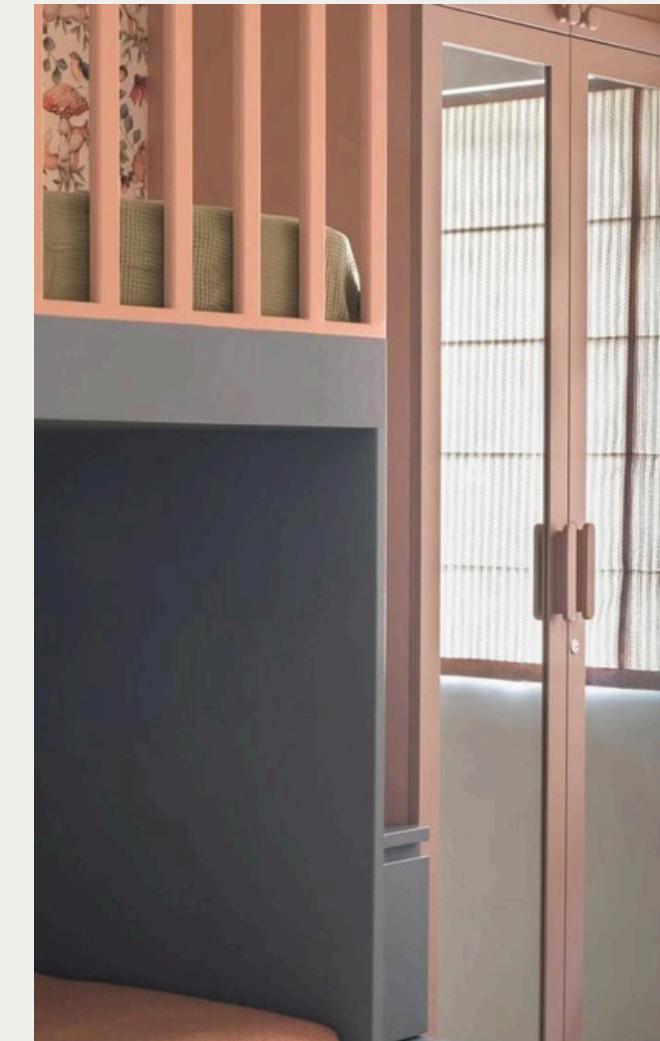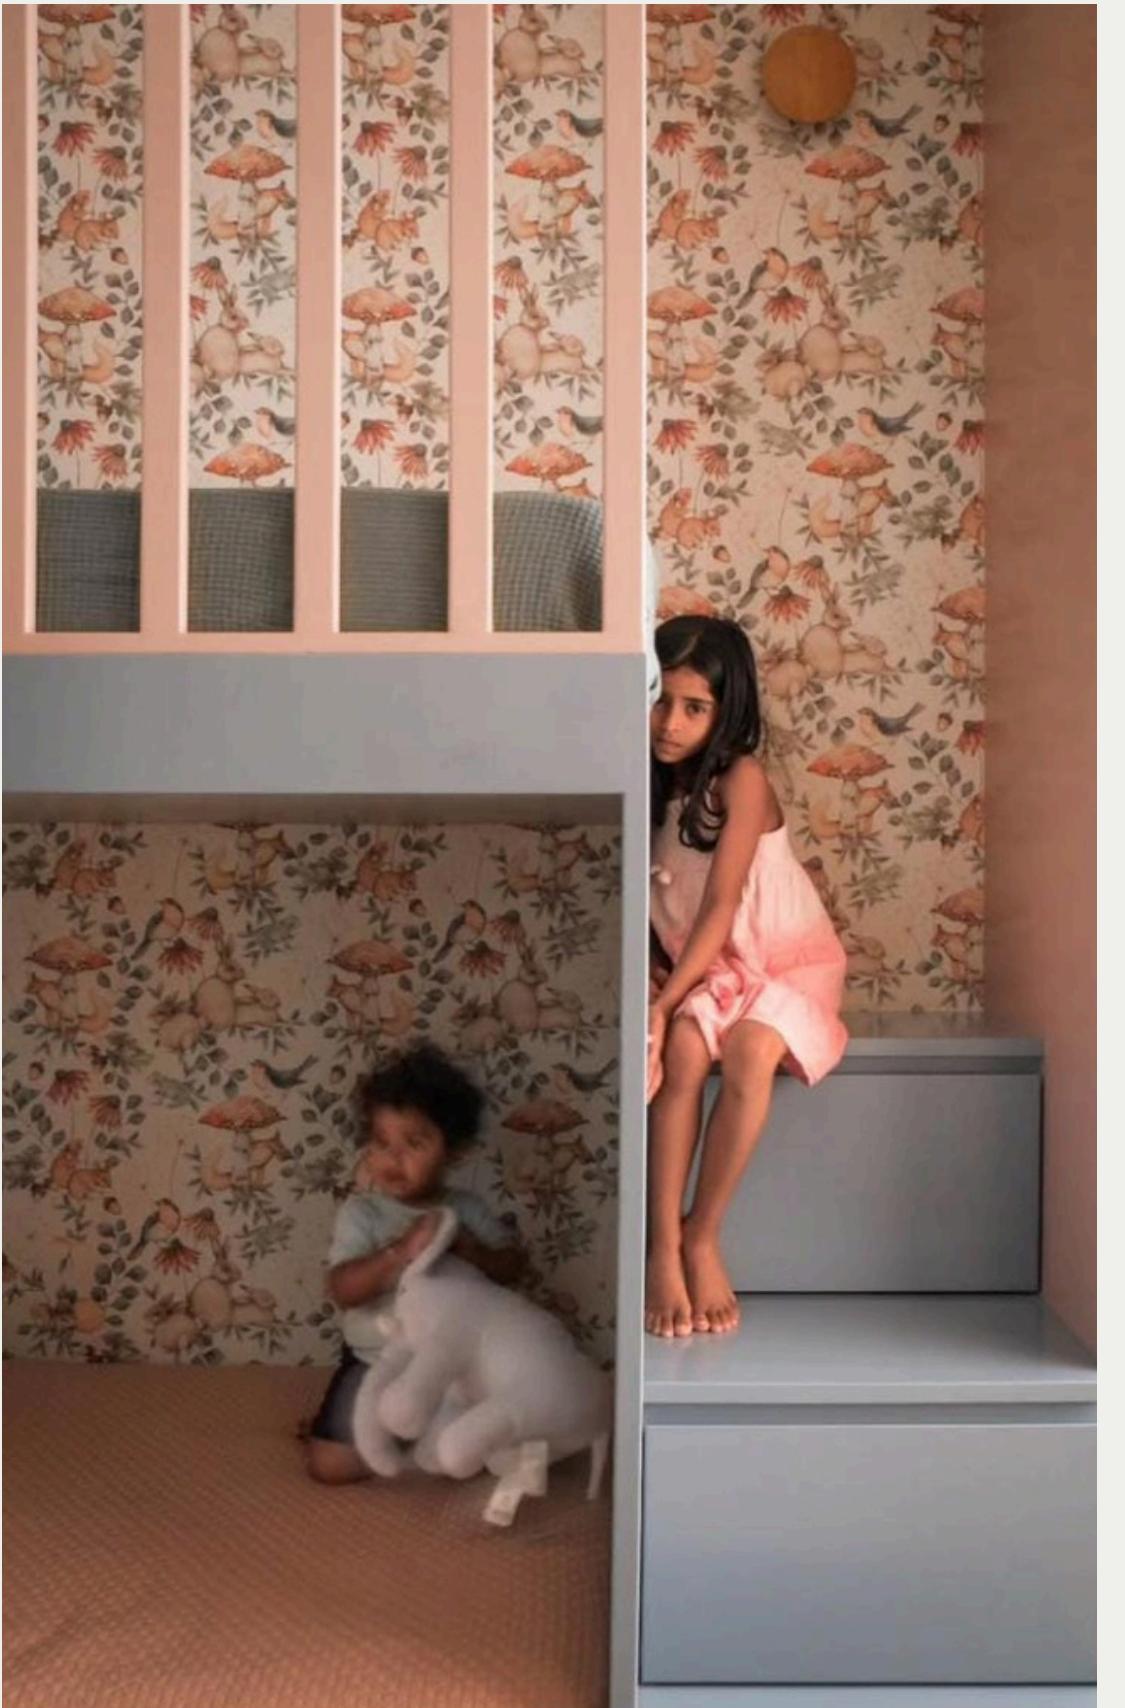

KIDS BEDROOM

2 SHOBA ROYAL PAVILION, BANGALORE

SHAMA & VERONIE



INTERIOR RENDERS

*PROJECT LEAD IN STUDIO SKAPA ARCHITECTS

3

RAJATHADRI, DHARMASTHALA

SHAMA & VERONIE




INTERIOR RENDERS


*PROJECT LEAD IN STUDIO SKAPA ARCHITECTS

4 SRINIVASA TEXTILE - WORK PODS, CHENNAI

SHAMA & VERONIE

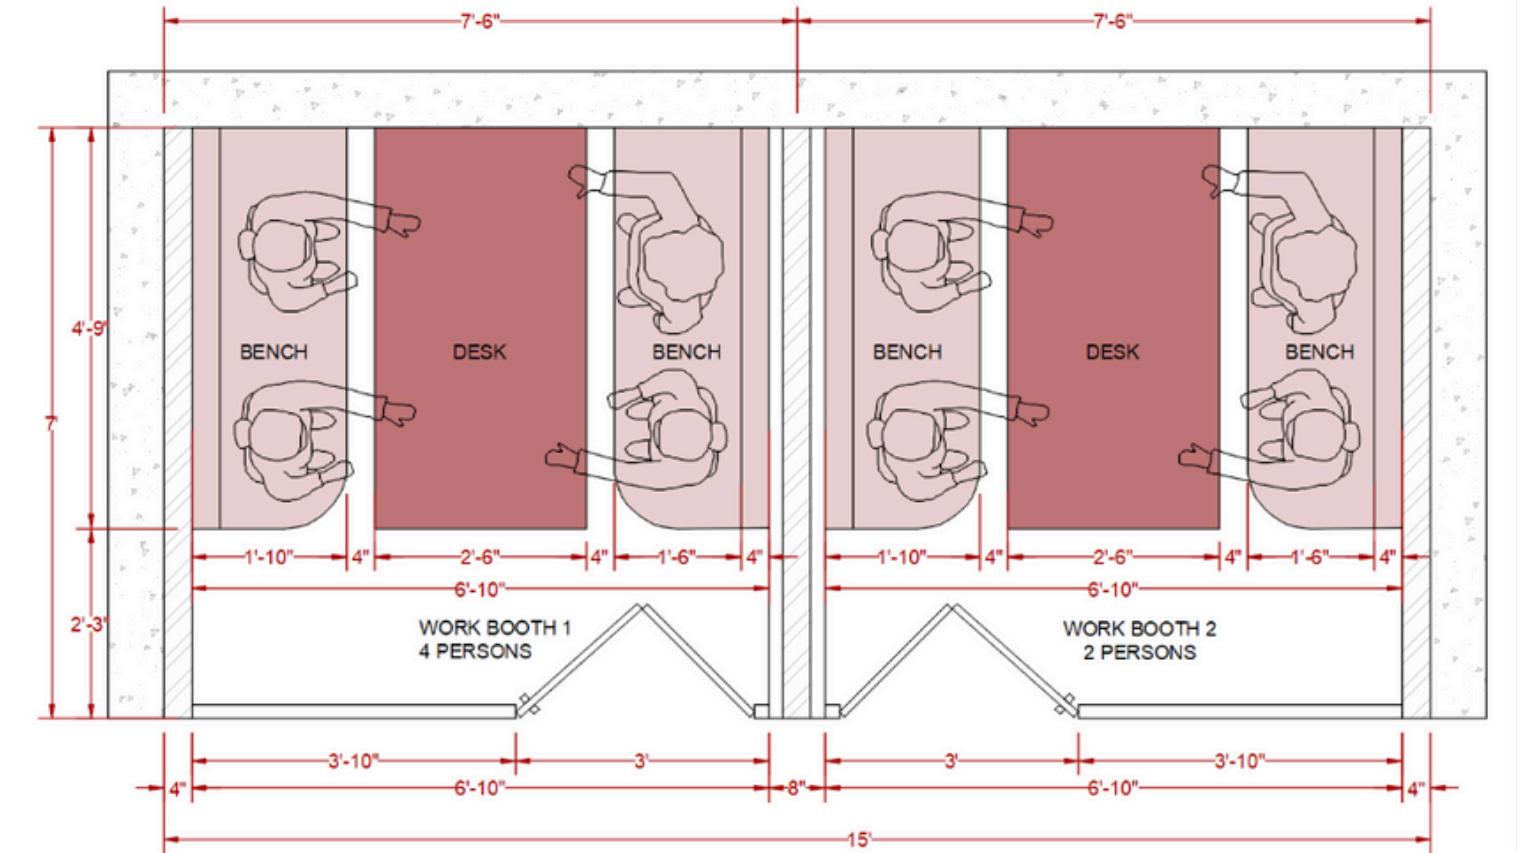



WORK POD 1

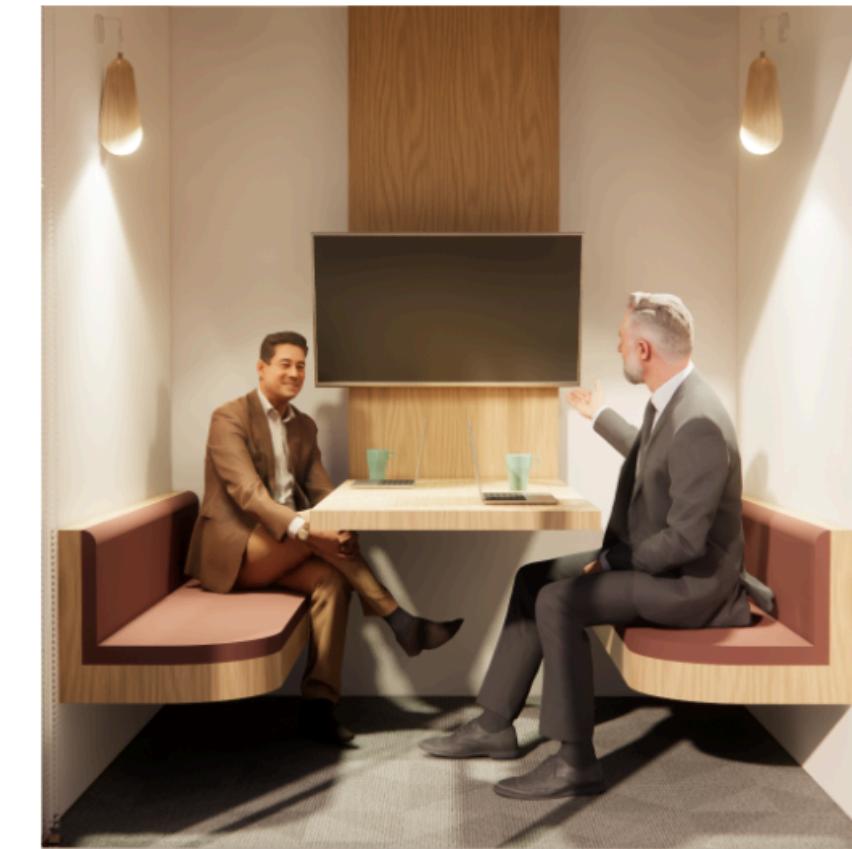


WORK POD 2

4 SRINIVASA TEXTILE - WORK PODS, CHENNAI


SHAMA & VERONIE

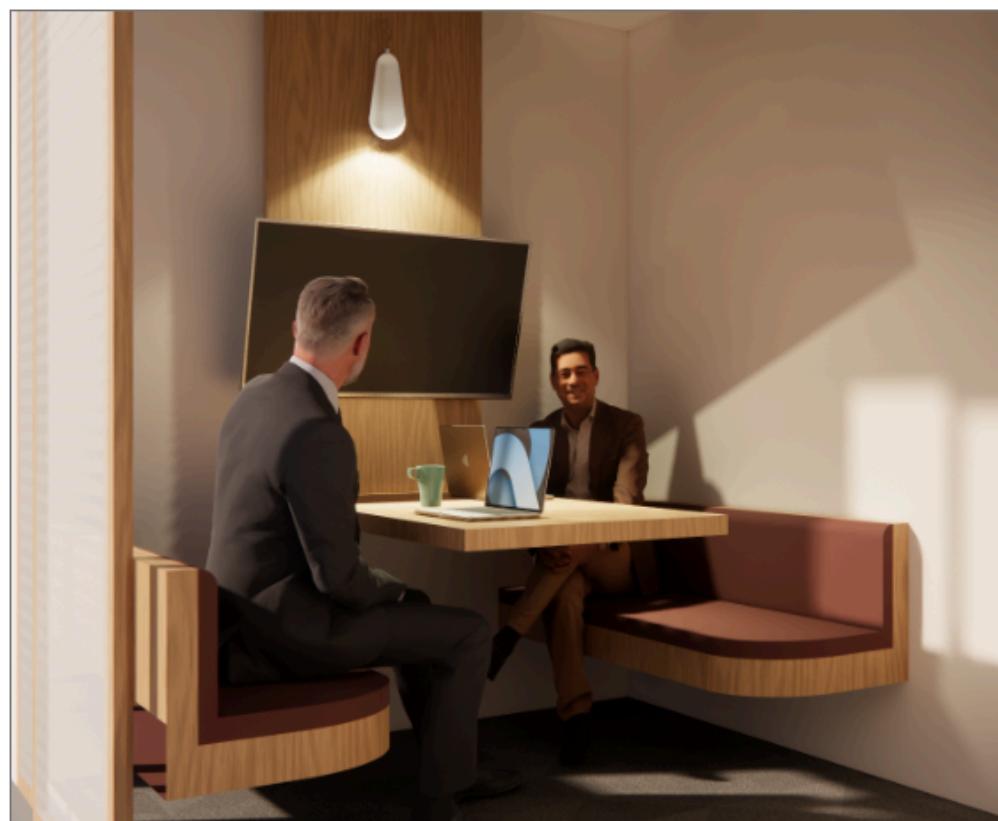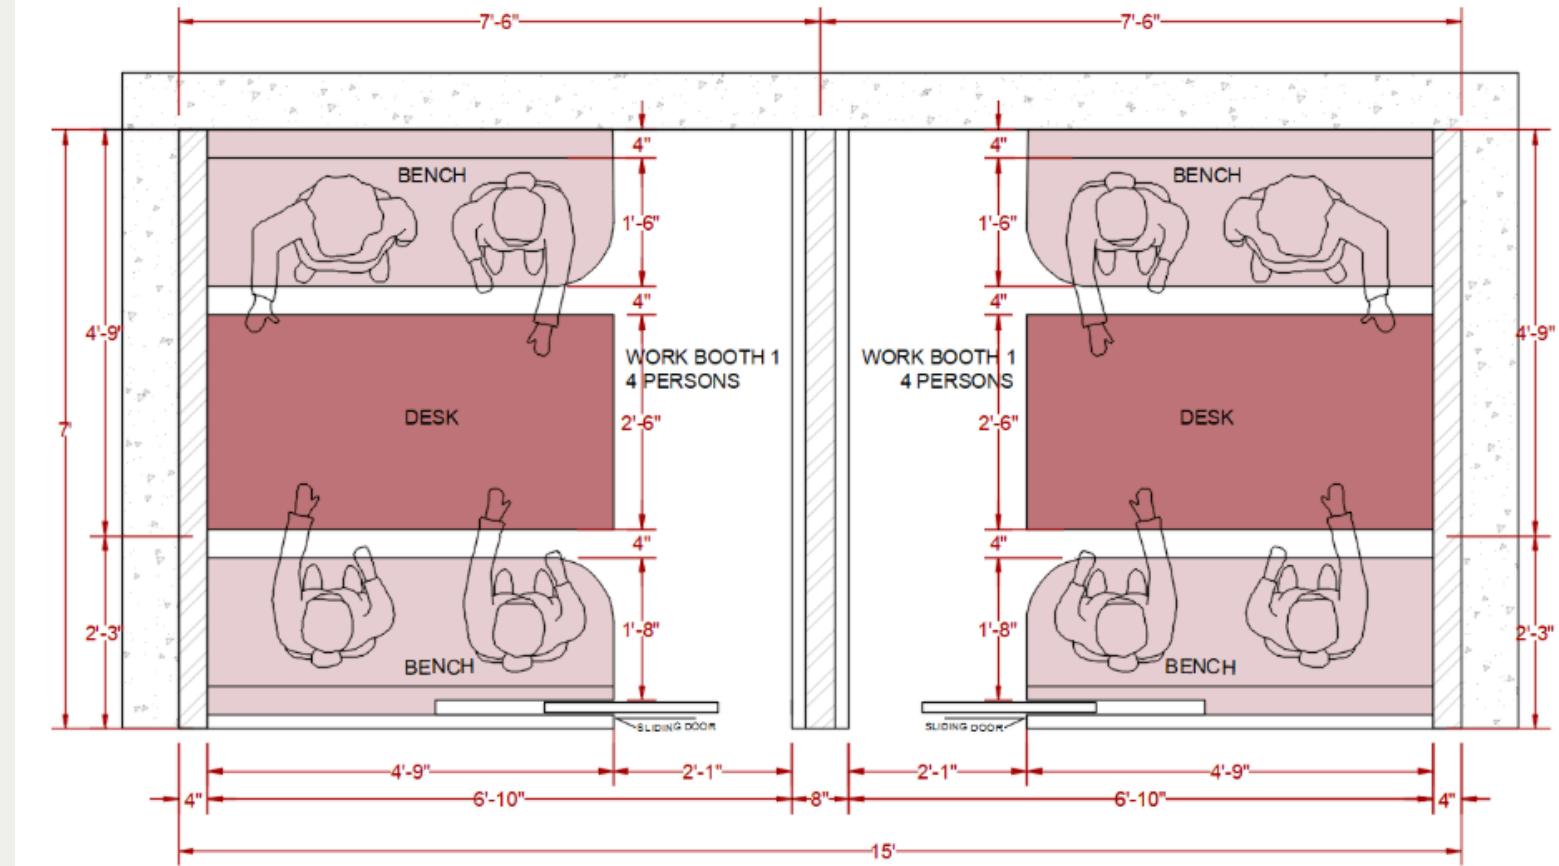

WORK POD 1

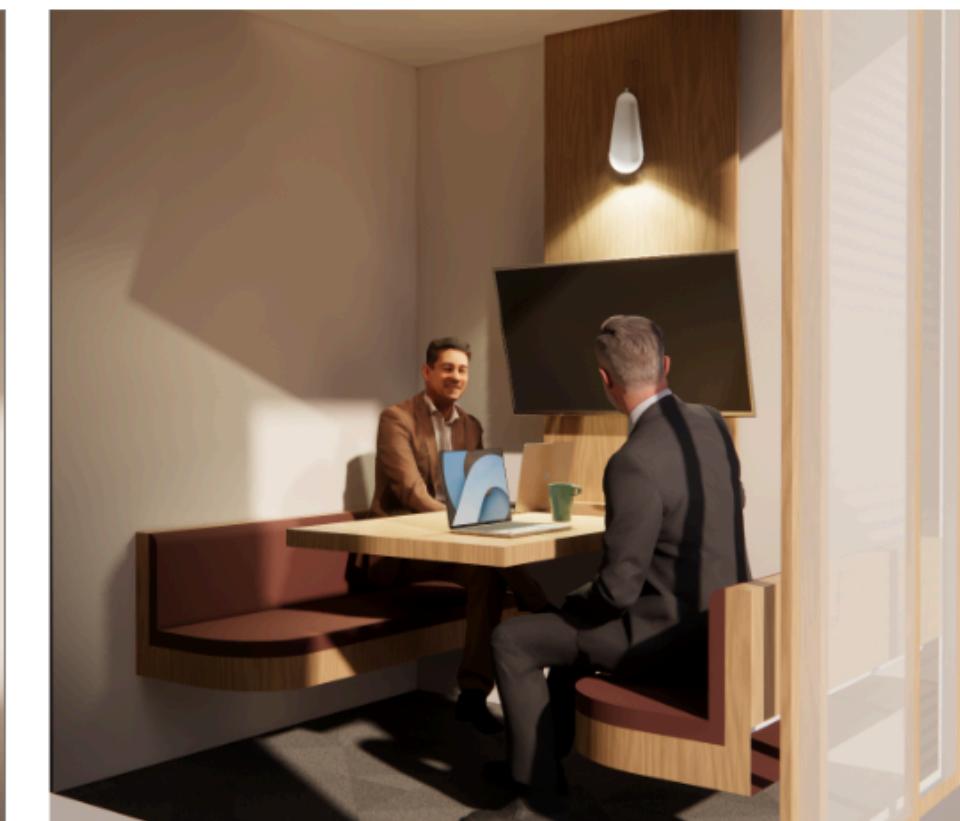

WORK POD 2


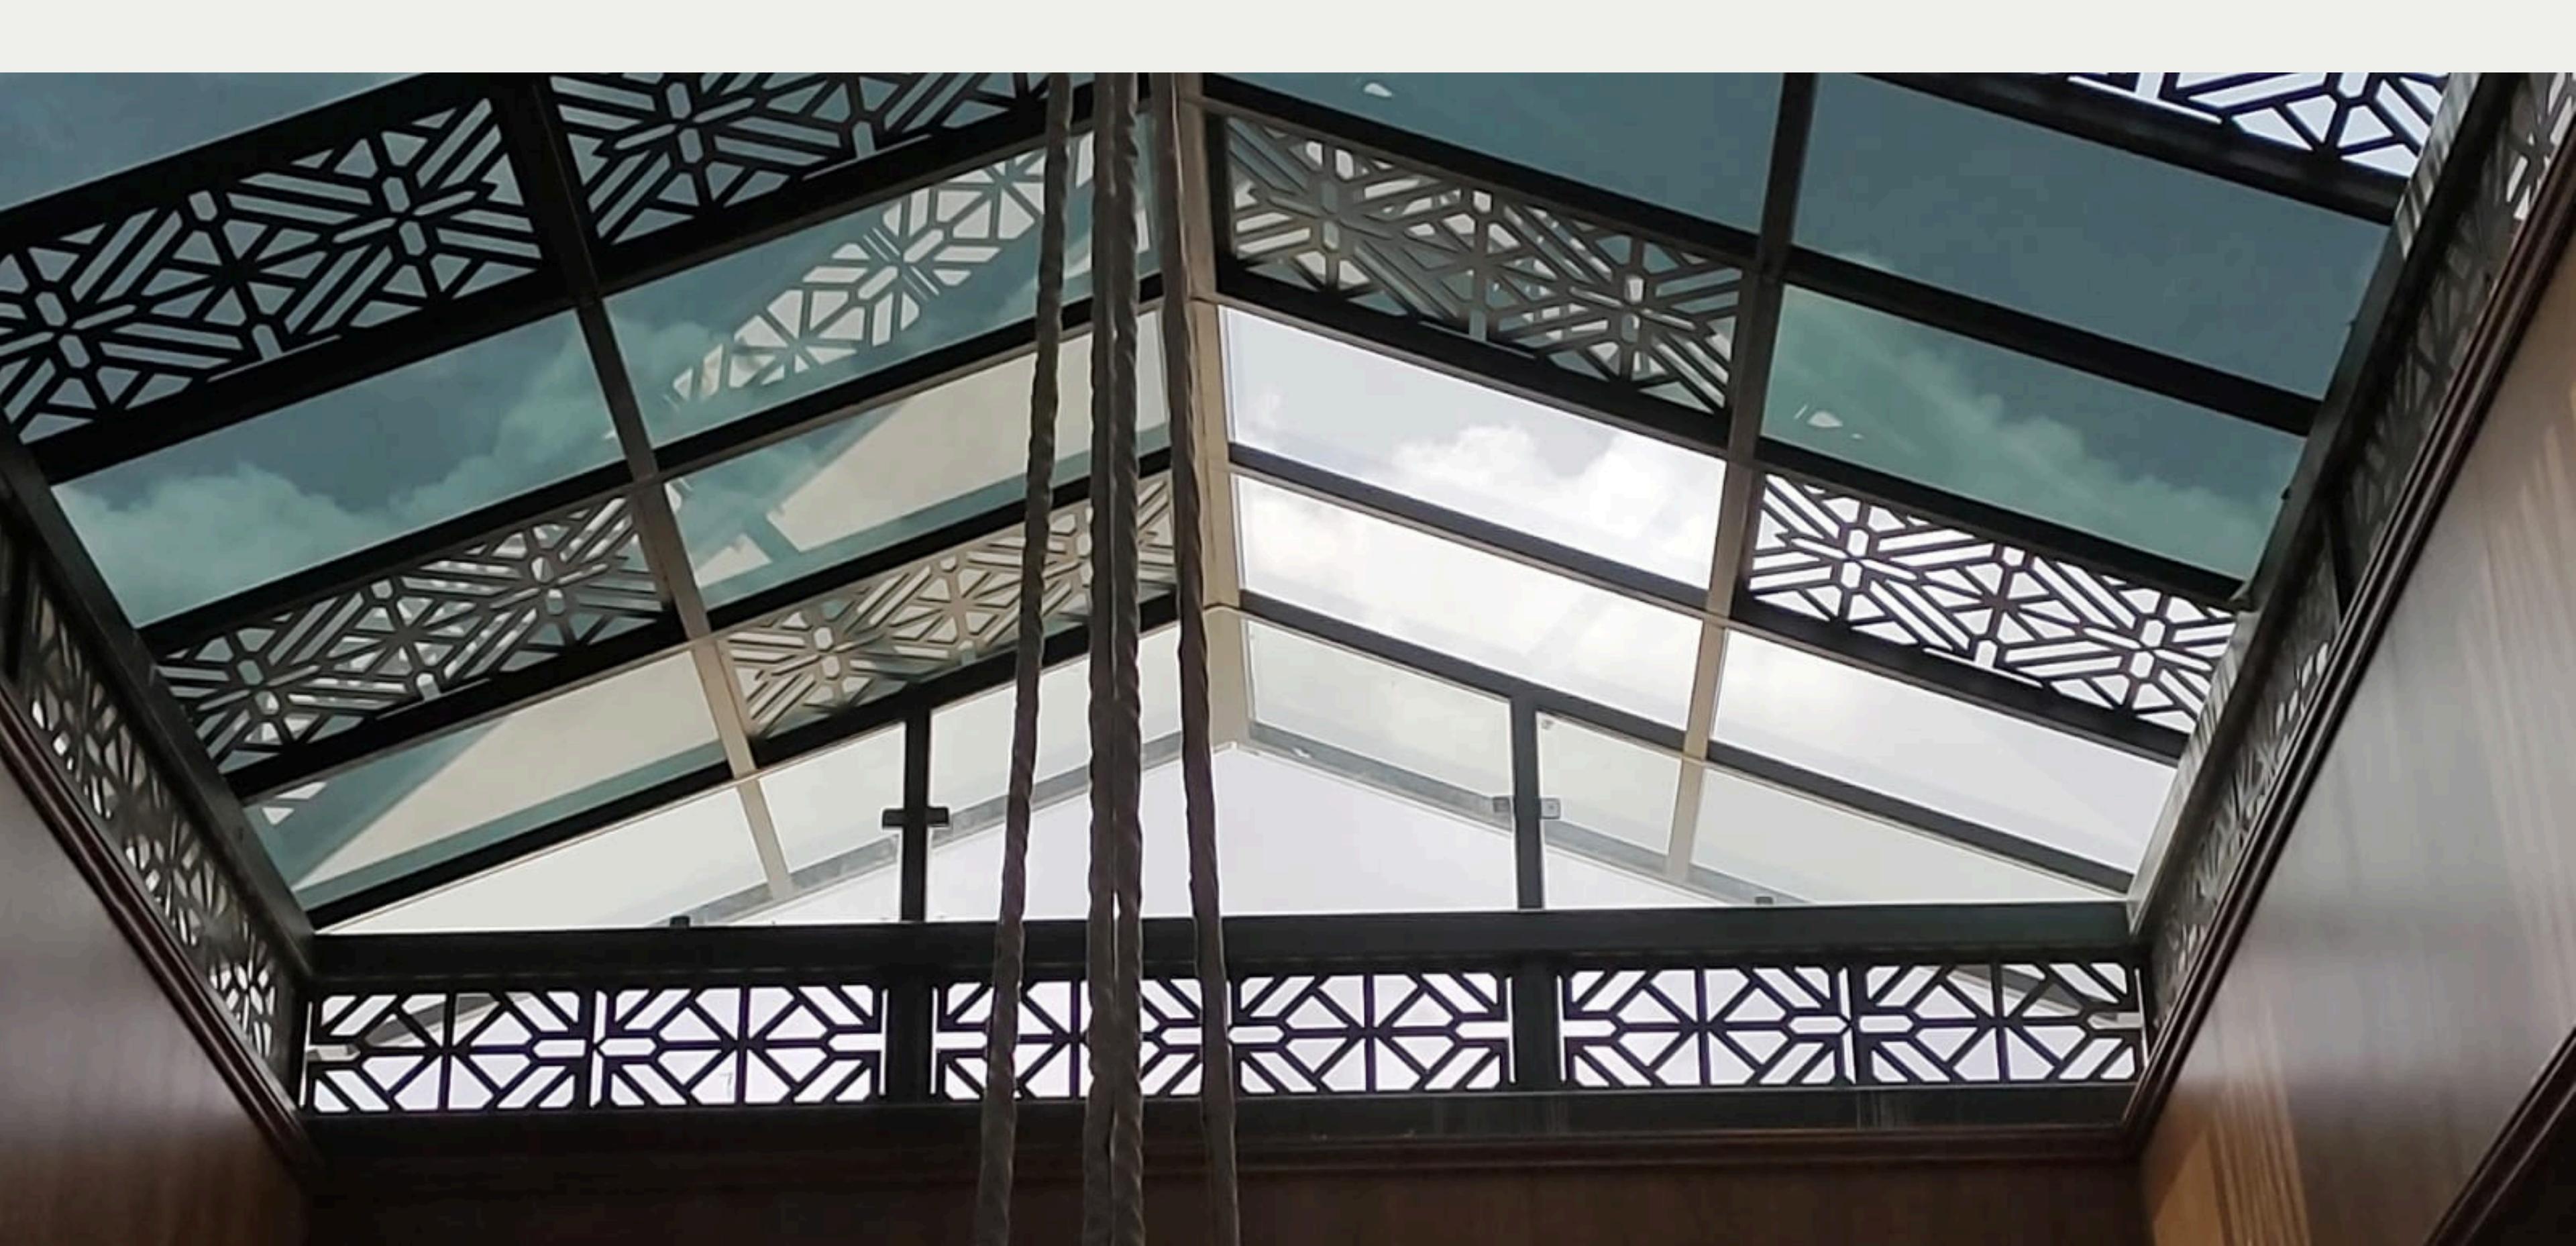


ARCHITECTURE

1


KESHAV MURTHY RESIDENCE, BANGALORE

SHAMA & VERONIE

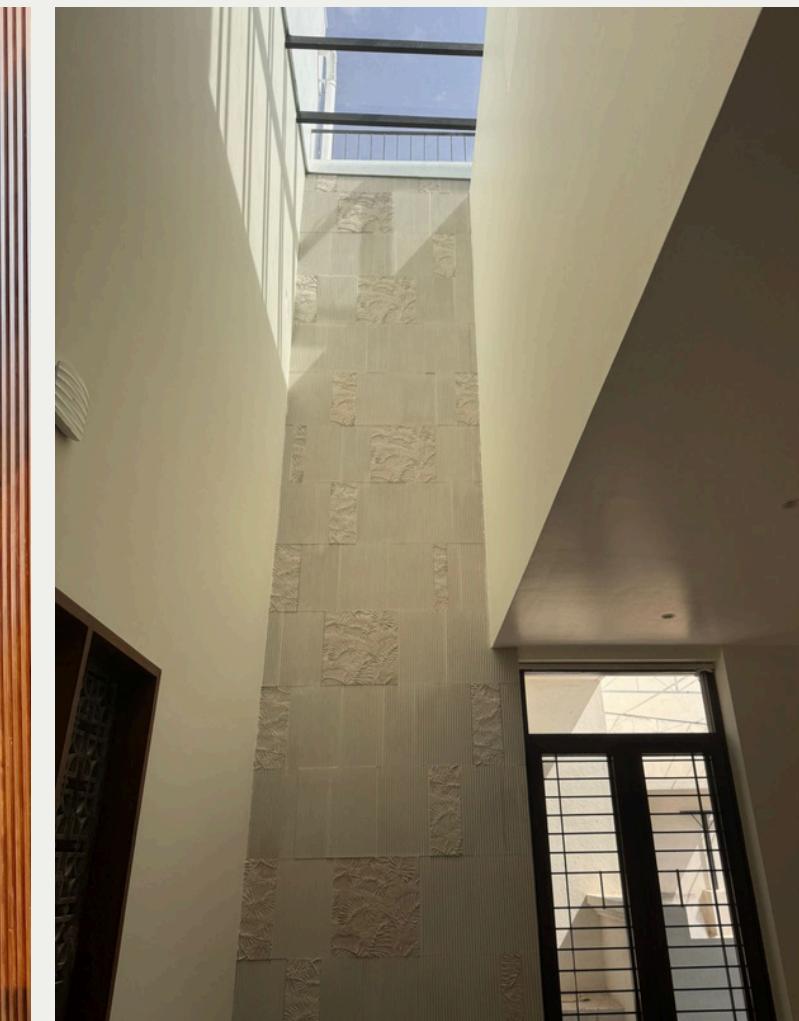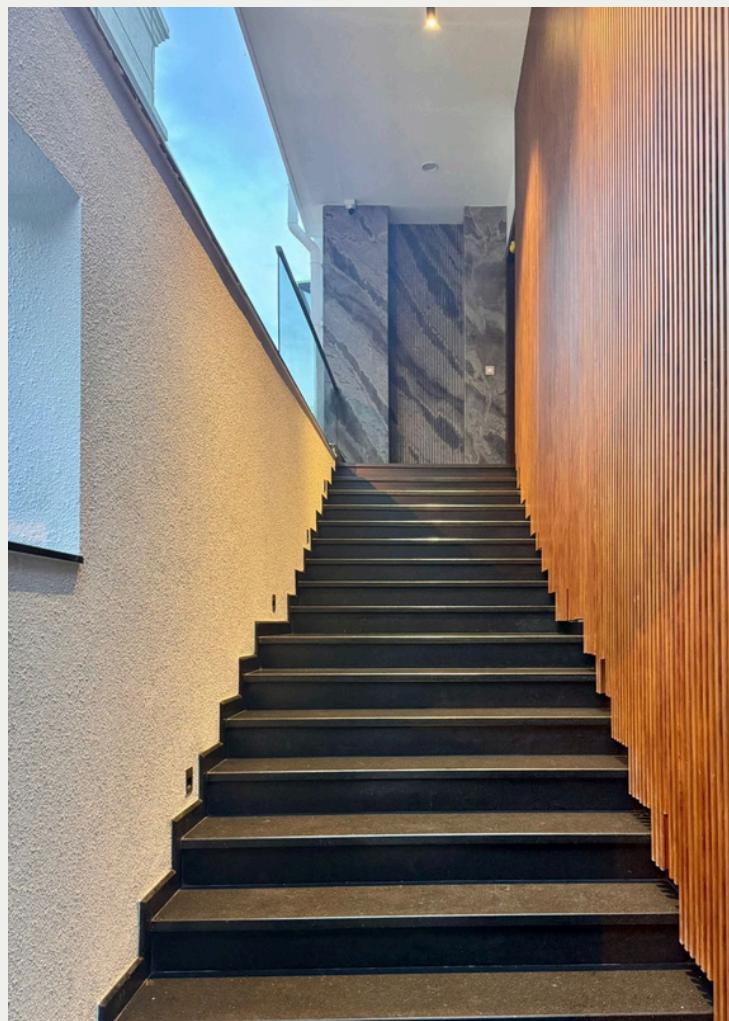


FACADE DETAILS

*PROJECT LEAD IN STUDIO SKAPA ARCHITECTS

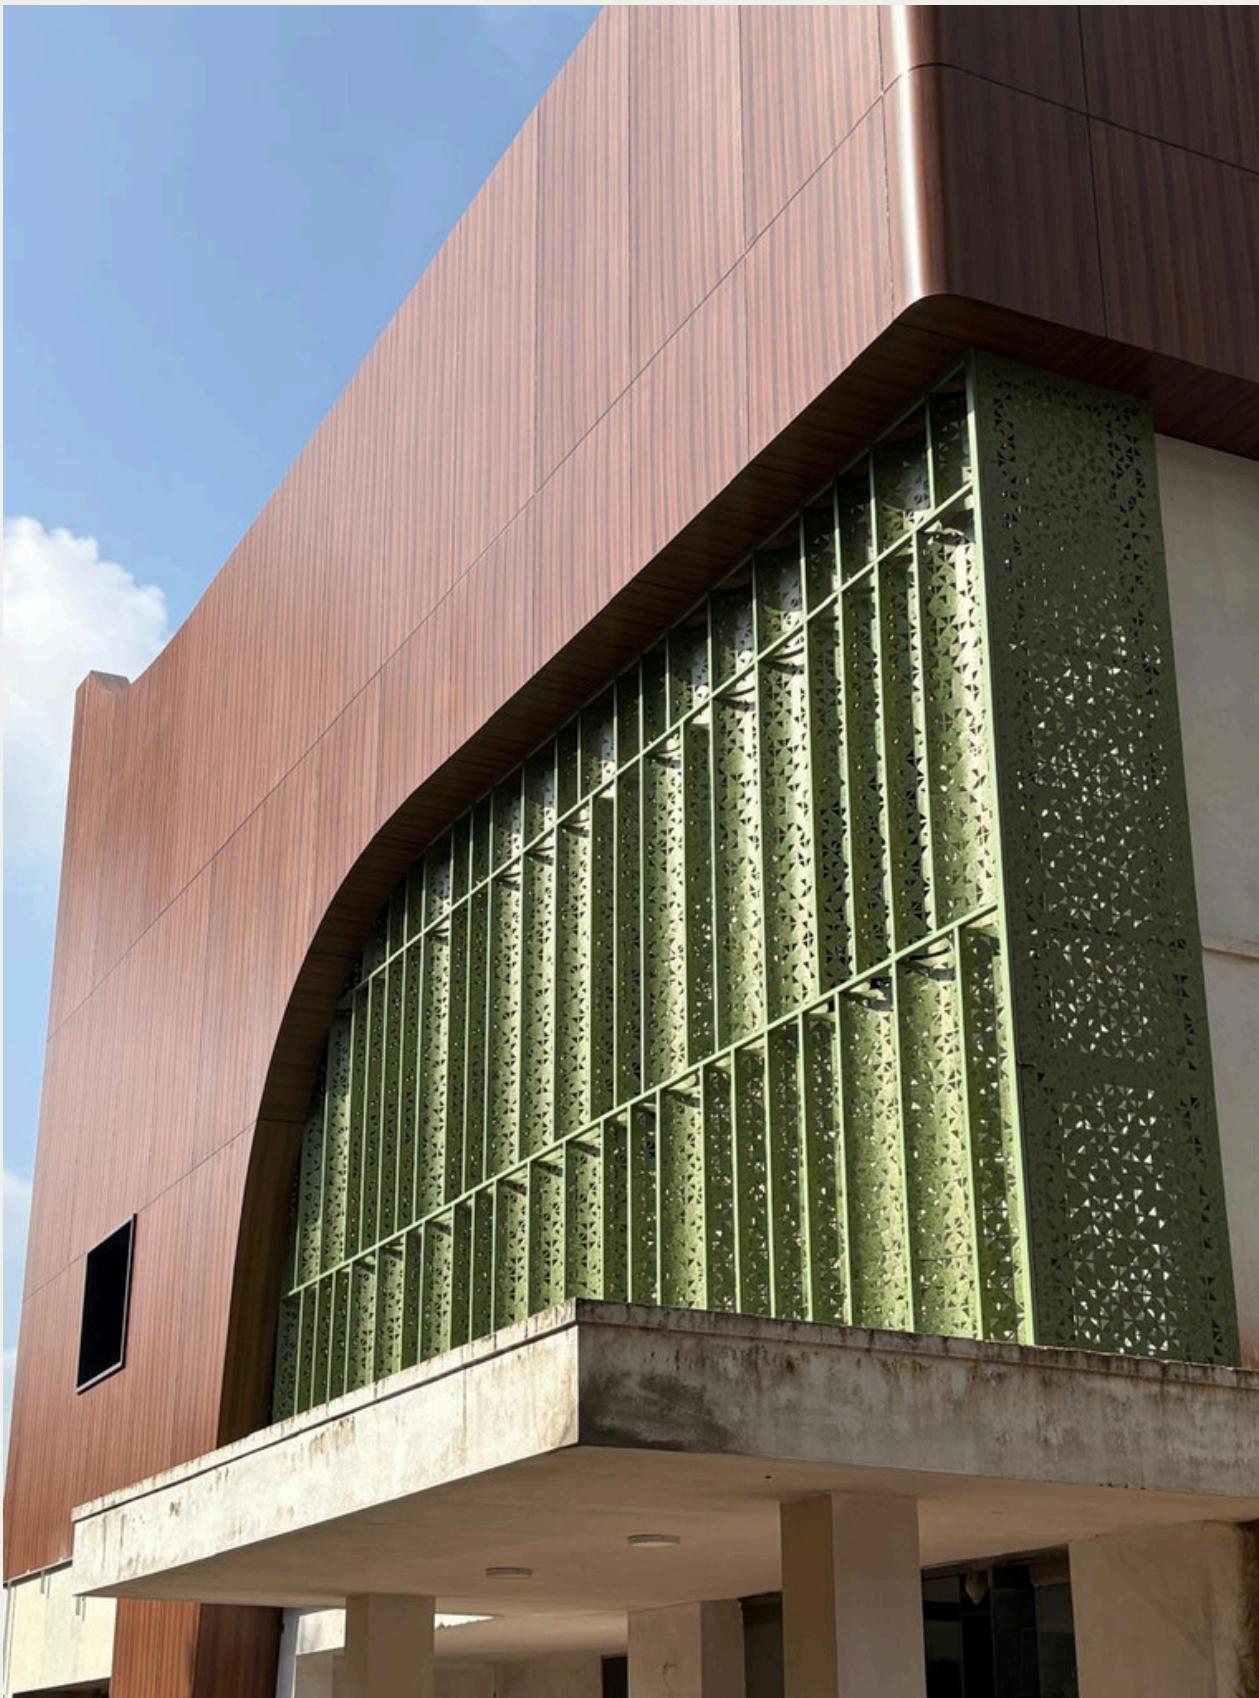

FAÇADE DETAILS

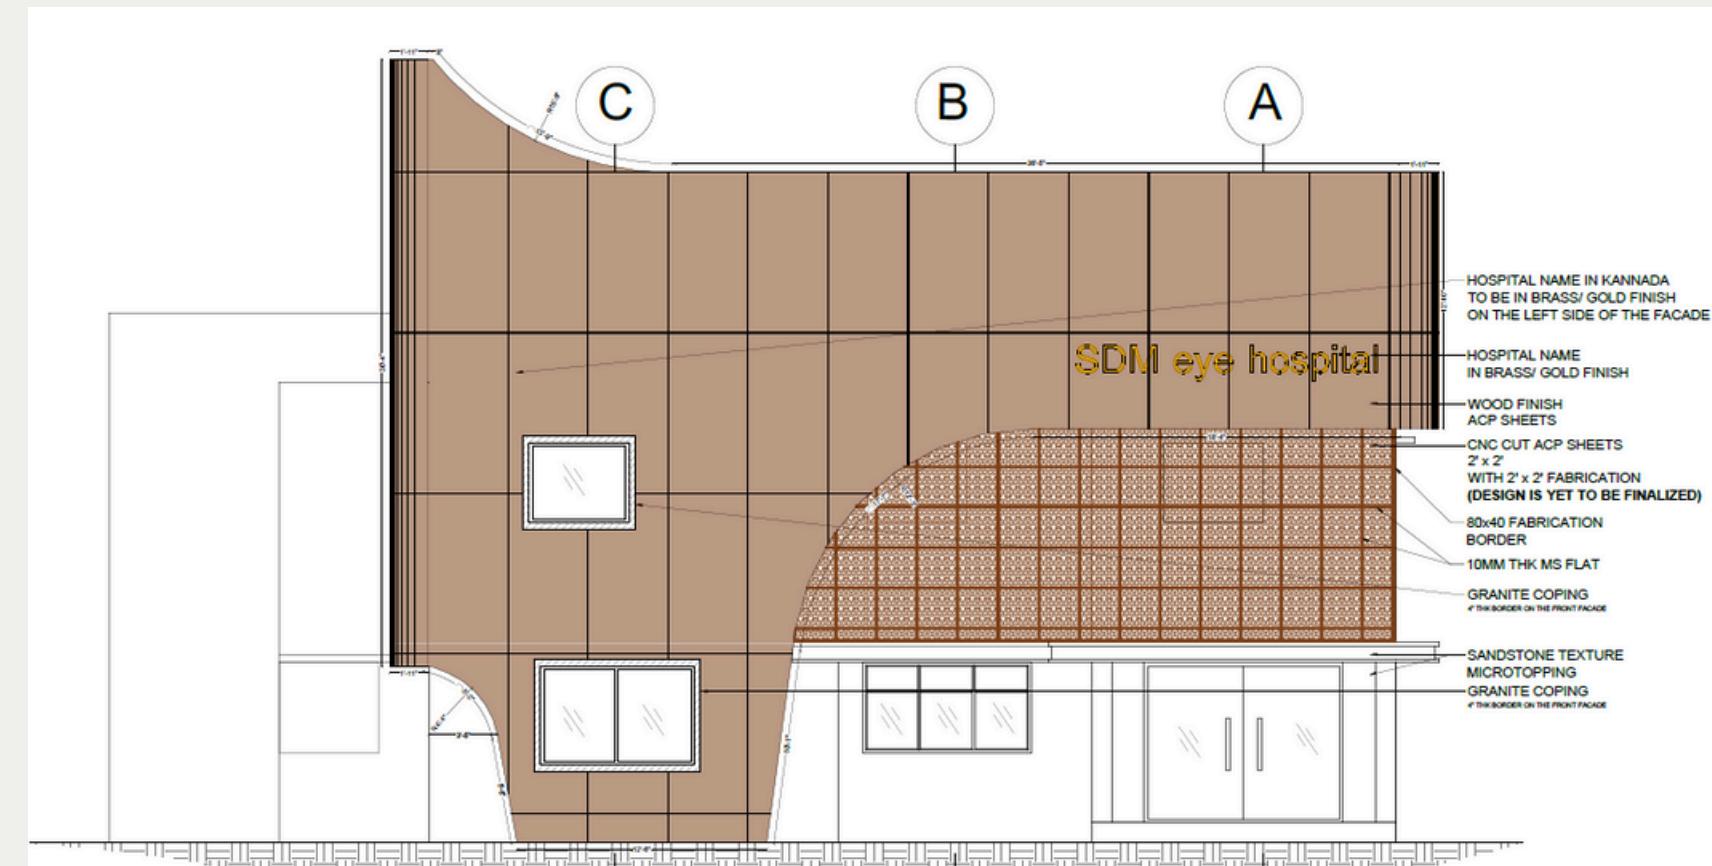

*PROJECT LEAD IN STUDIO SKAPA ARCHITECTS

3

VEERABHAVANA, MANGALORE

SHAMA & VERONIE



FACADE DETAILS





*PROJECT LEAD IN STUDIO SKAPA ARCHITECTS

3

VEERABHAVANA, MANGALORE

SHAMA & VERONIE

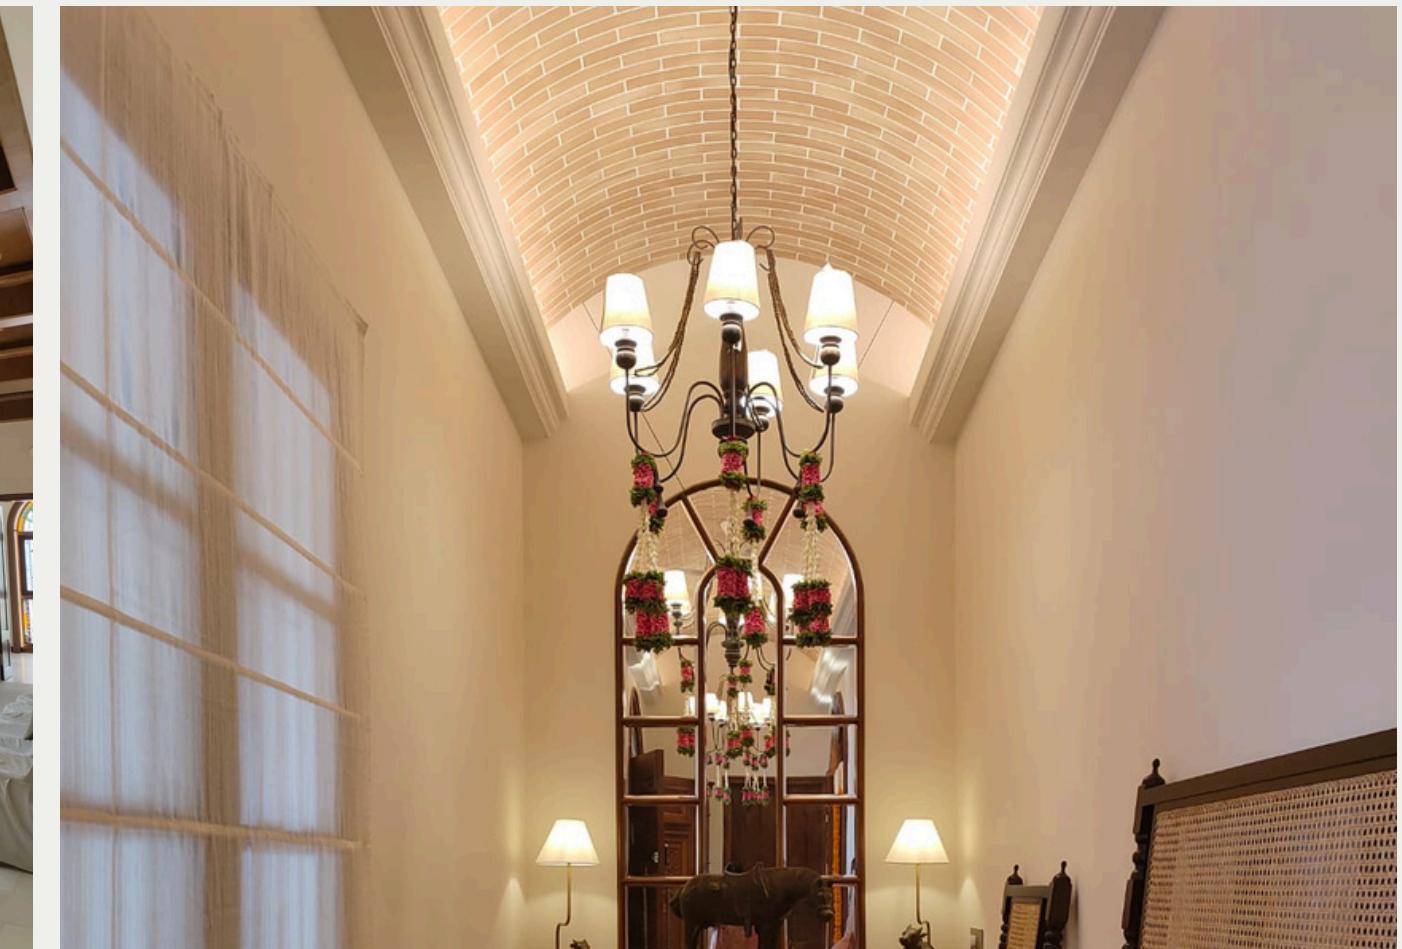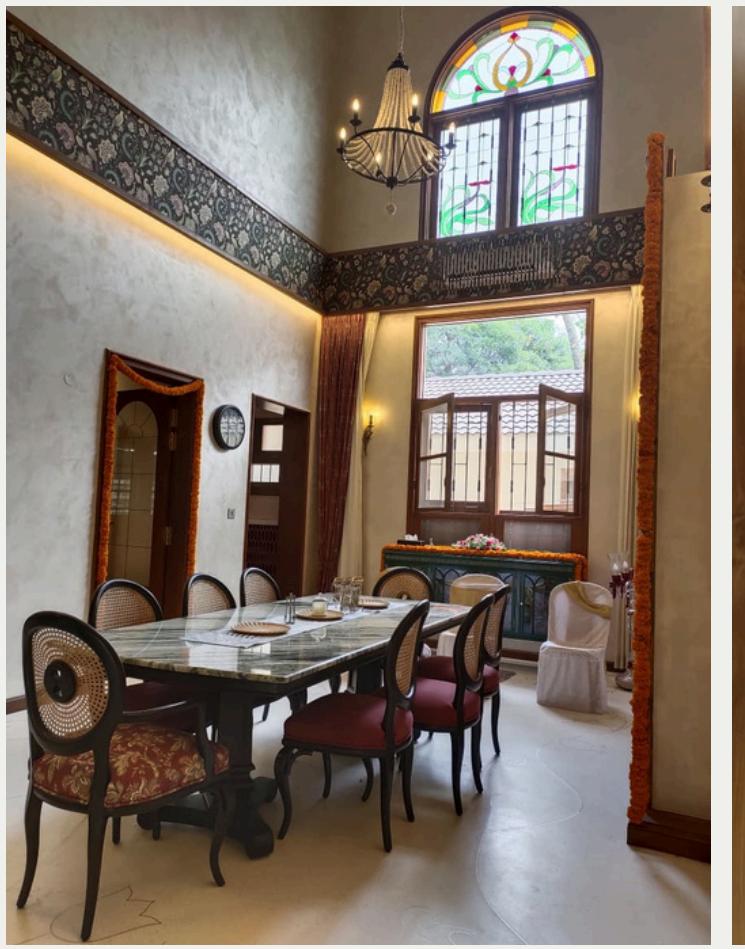

INTERIORS

*PROJECT LEAD IN STUDIO SKAPA ARCHITECTS



RENOVATION



KITCHEN - EXISTING





KITCHEN - WORK IN PROGRESS

2


KSE FARM HOUSE, HYDERABAD

SHAMA & VERONIE

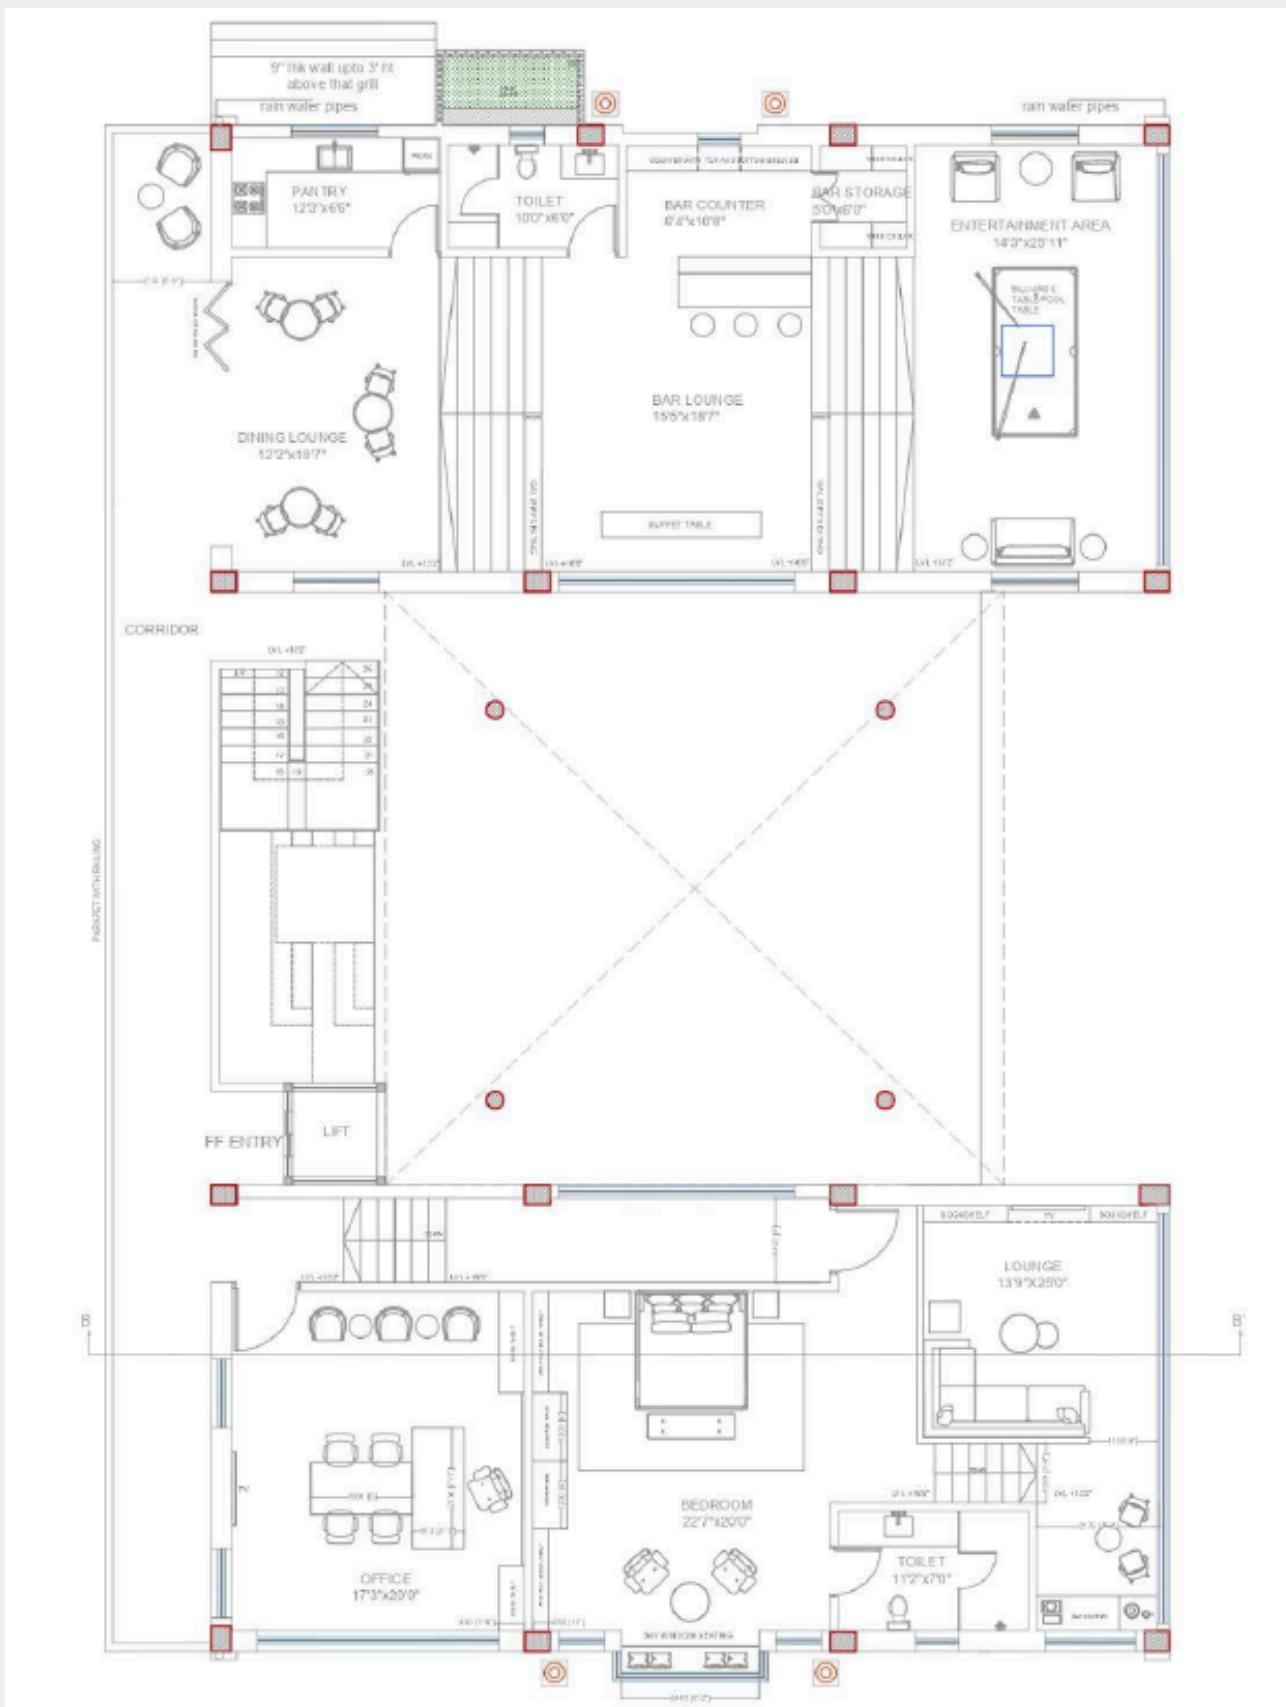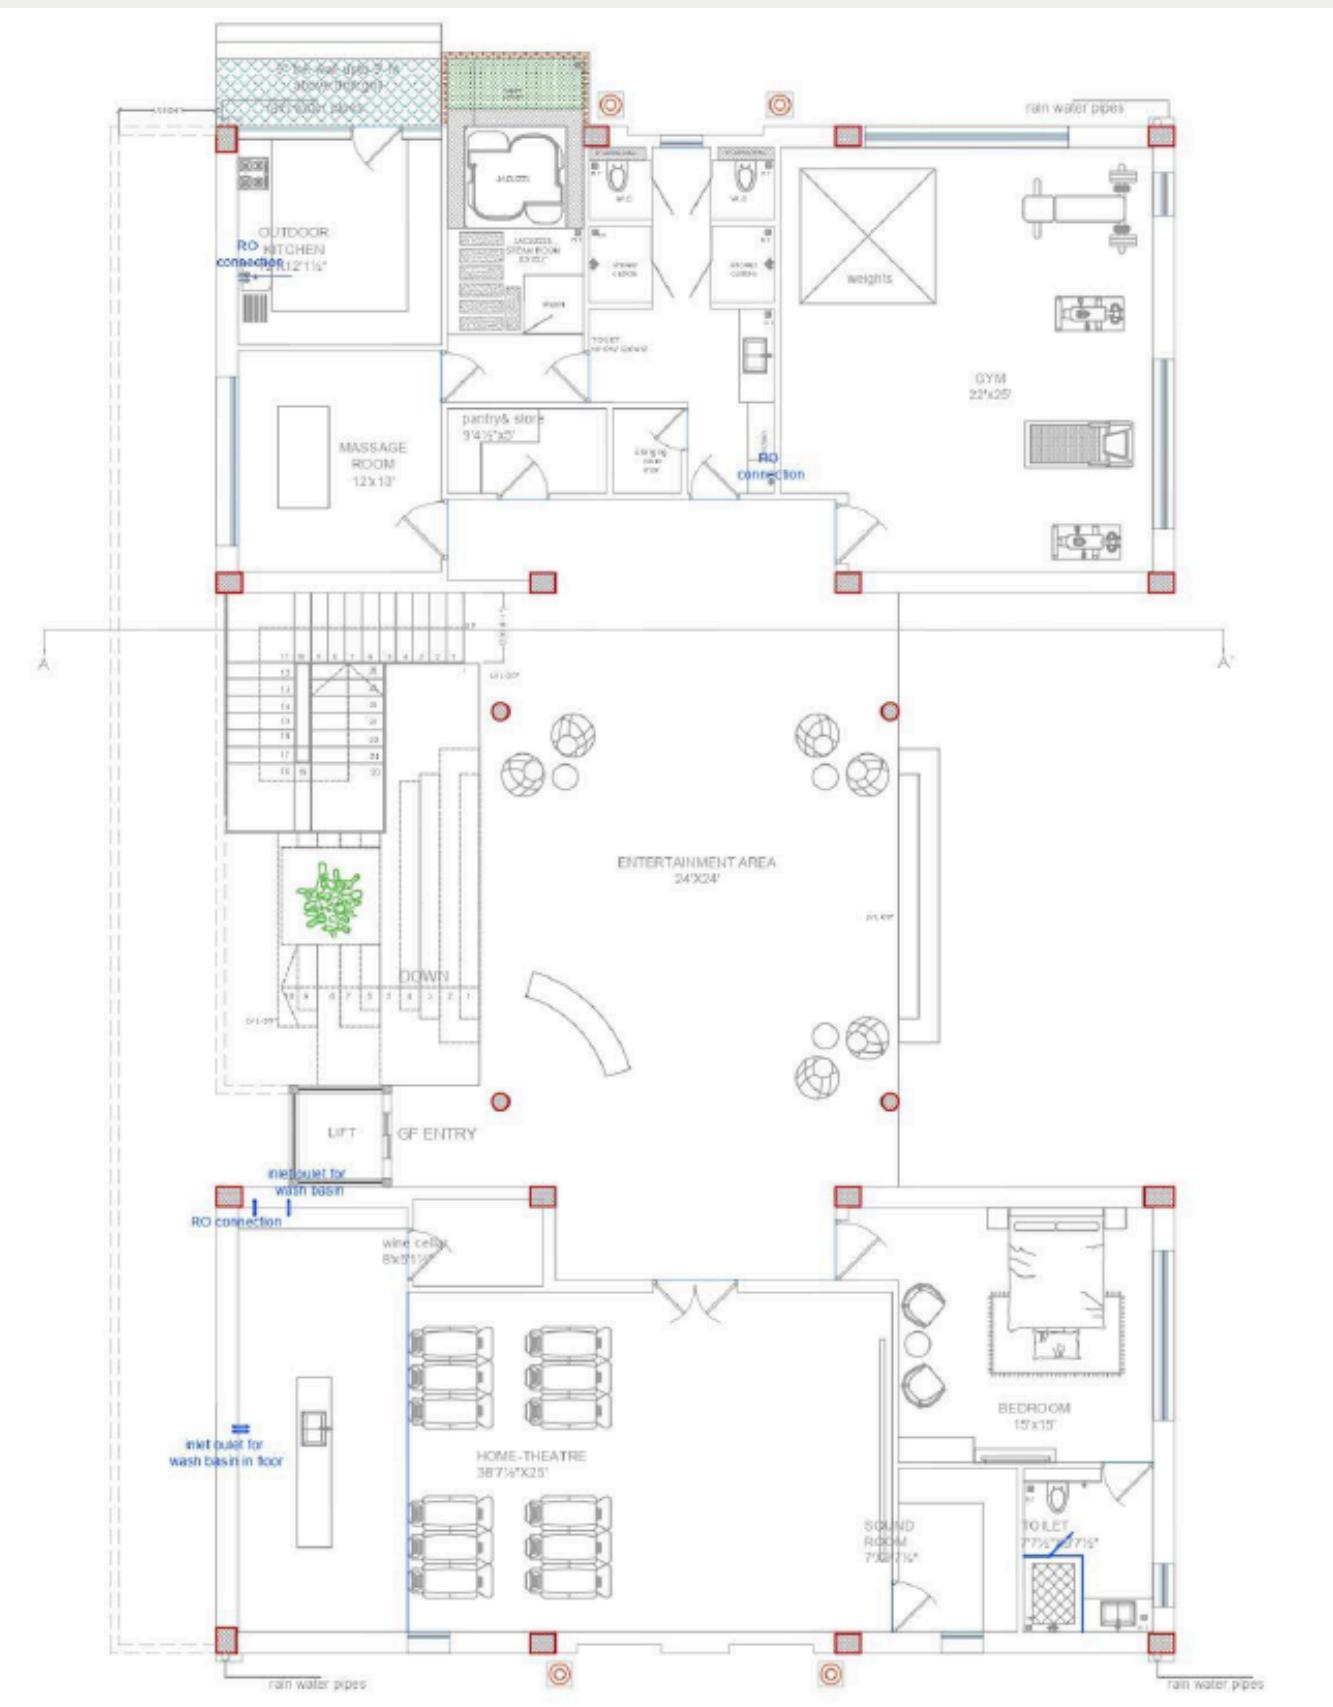

PLANS



*PROJECT LEAD IN STUDIO SKAPA ARCHITECTS

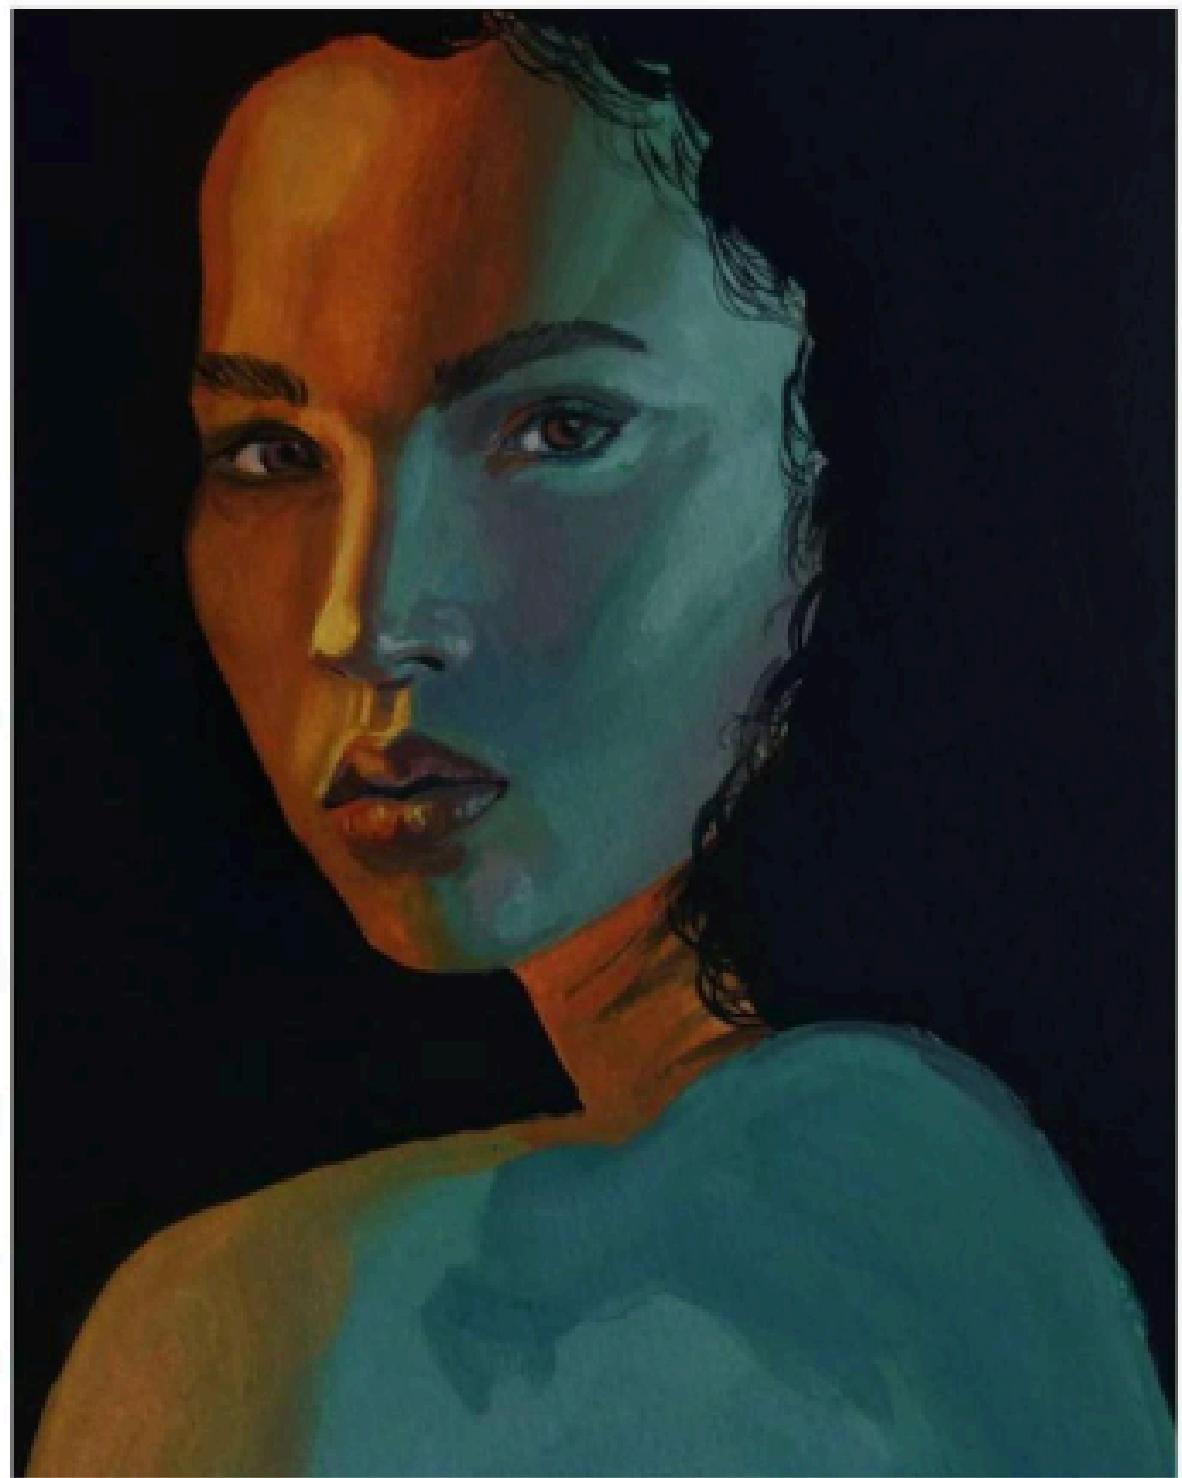


ART

1 THE ENTRANCE CAFE - ART WORK

SHAMA & VERONIE

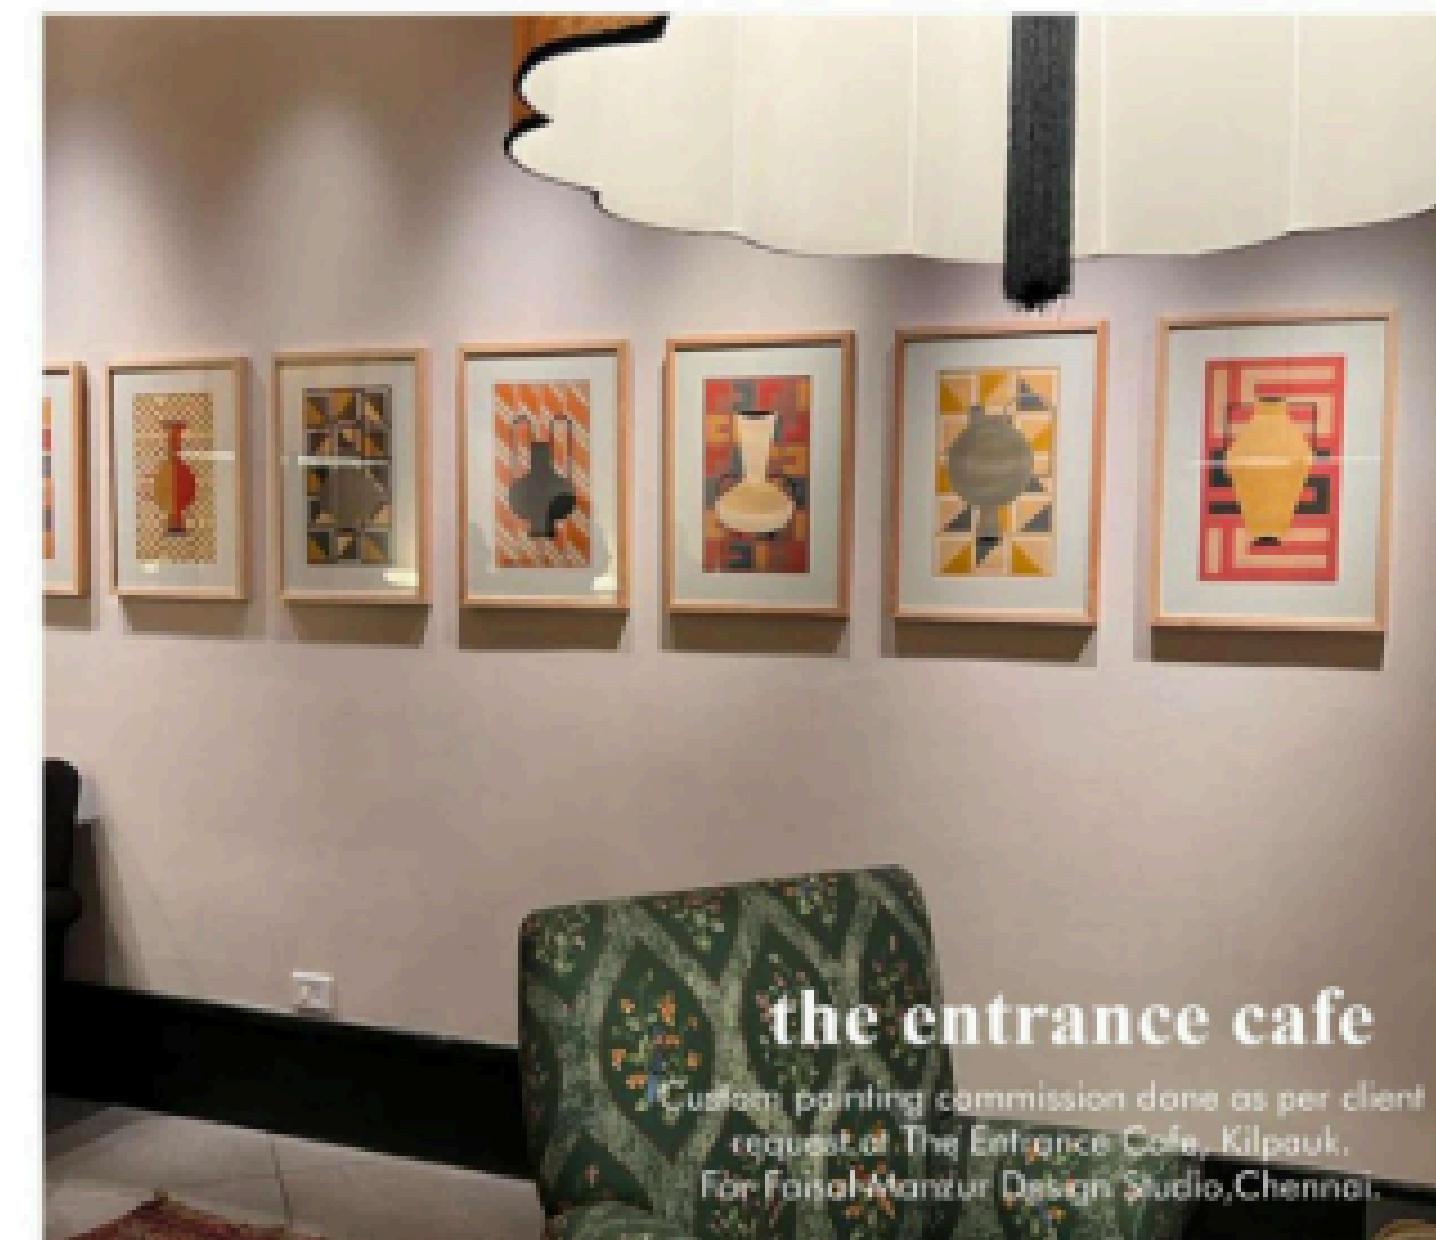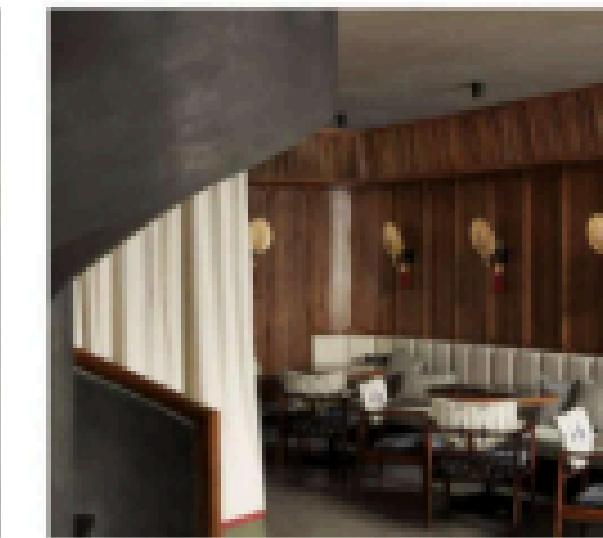

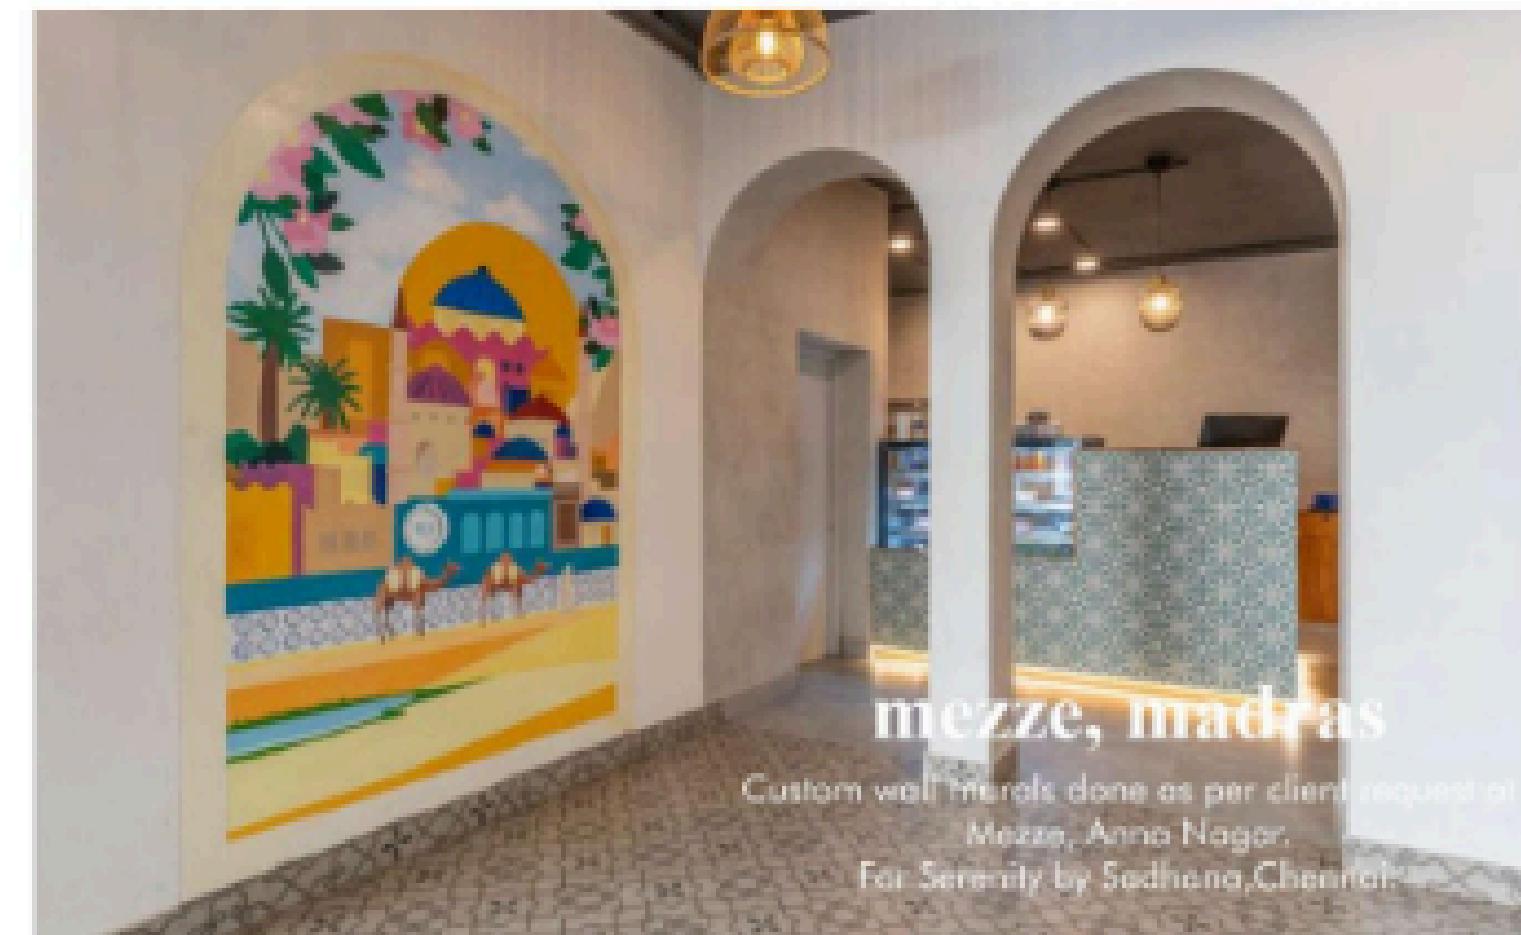

Contact



Phone : 9611211509/ 8056276496

Email : shamaandveronie@gmail.com

THANK YOU